مشروع حدائق الفسطاط — المرحلة الثانية

منطقة الحدائق التراثية • البند SF-12: المزولة الشمسية

التصميم (أ): المزولة الجامعة

مسقط التوقيع والنقاط المرجعية

التوقيع بالإحداثيات المحلية والشبكية
الشمال الحقيقي إلى أعلى اللوحة

ملاحظات

- الإحداثيات المحلية: الأصل مركز الدائرة، x شرقًا، y نحو الشمال الحقيقي. الإحداثيات الشبكية: حزام مصر الأحمر (EPSG:22992).
- تقارب الشبكة γ = 0.1214°: الشمال الشبكي شرق الحقيقي؛ E = E0 + x·cosγ − y·sinγ ، N = N0 + y·cosγ + x·sinγ.
- يُثبَّت P0 وP7 وP8 أولًا بجهاز GNSS (RTK) أو محطة شاملة، ويُتحقق من خط الزوال بالرصد الشمسي (اللوحة E-05).
- منسوب التشطيب ±0.00 لكل الدائرة (الوجه والحلقة)، ويرتفع 180 مم عن منسوب الممر المحيط.
- ألواح الوجه 12 × 8 لوحًا مقاس 950 × 700 × 40 مم.
- الأبعاد بالمتر ما لم يُذكر غير ذلك.

خط الزوال (الشمال الحقيقي)

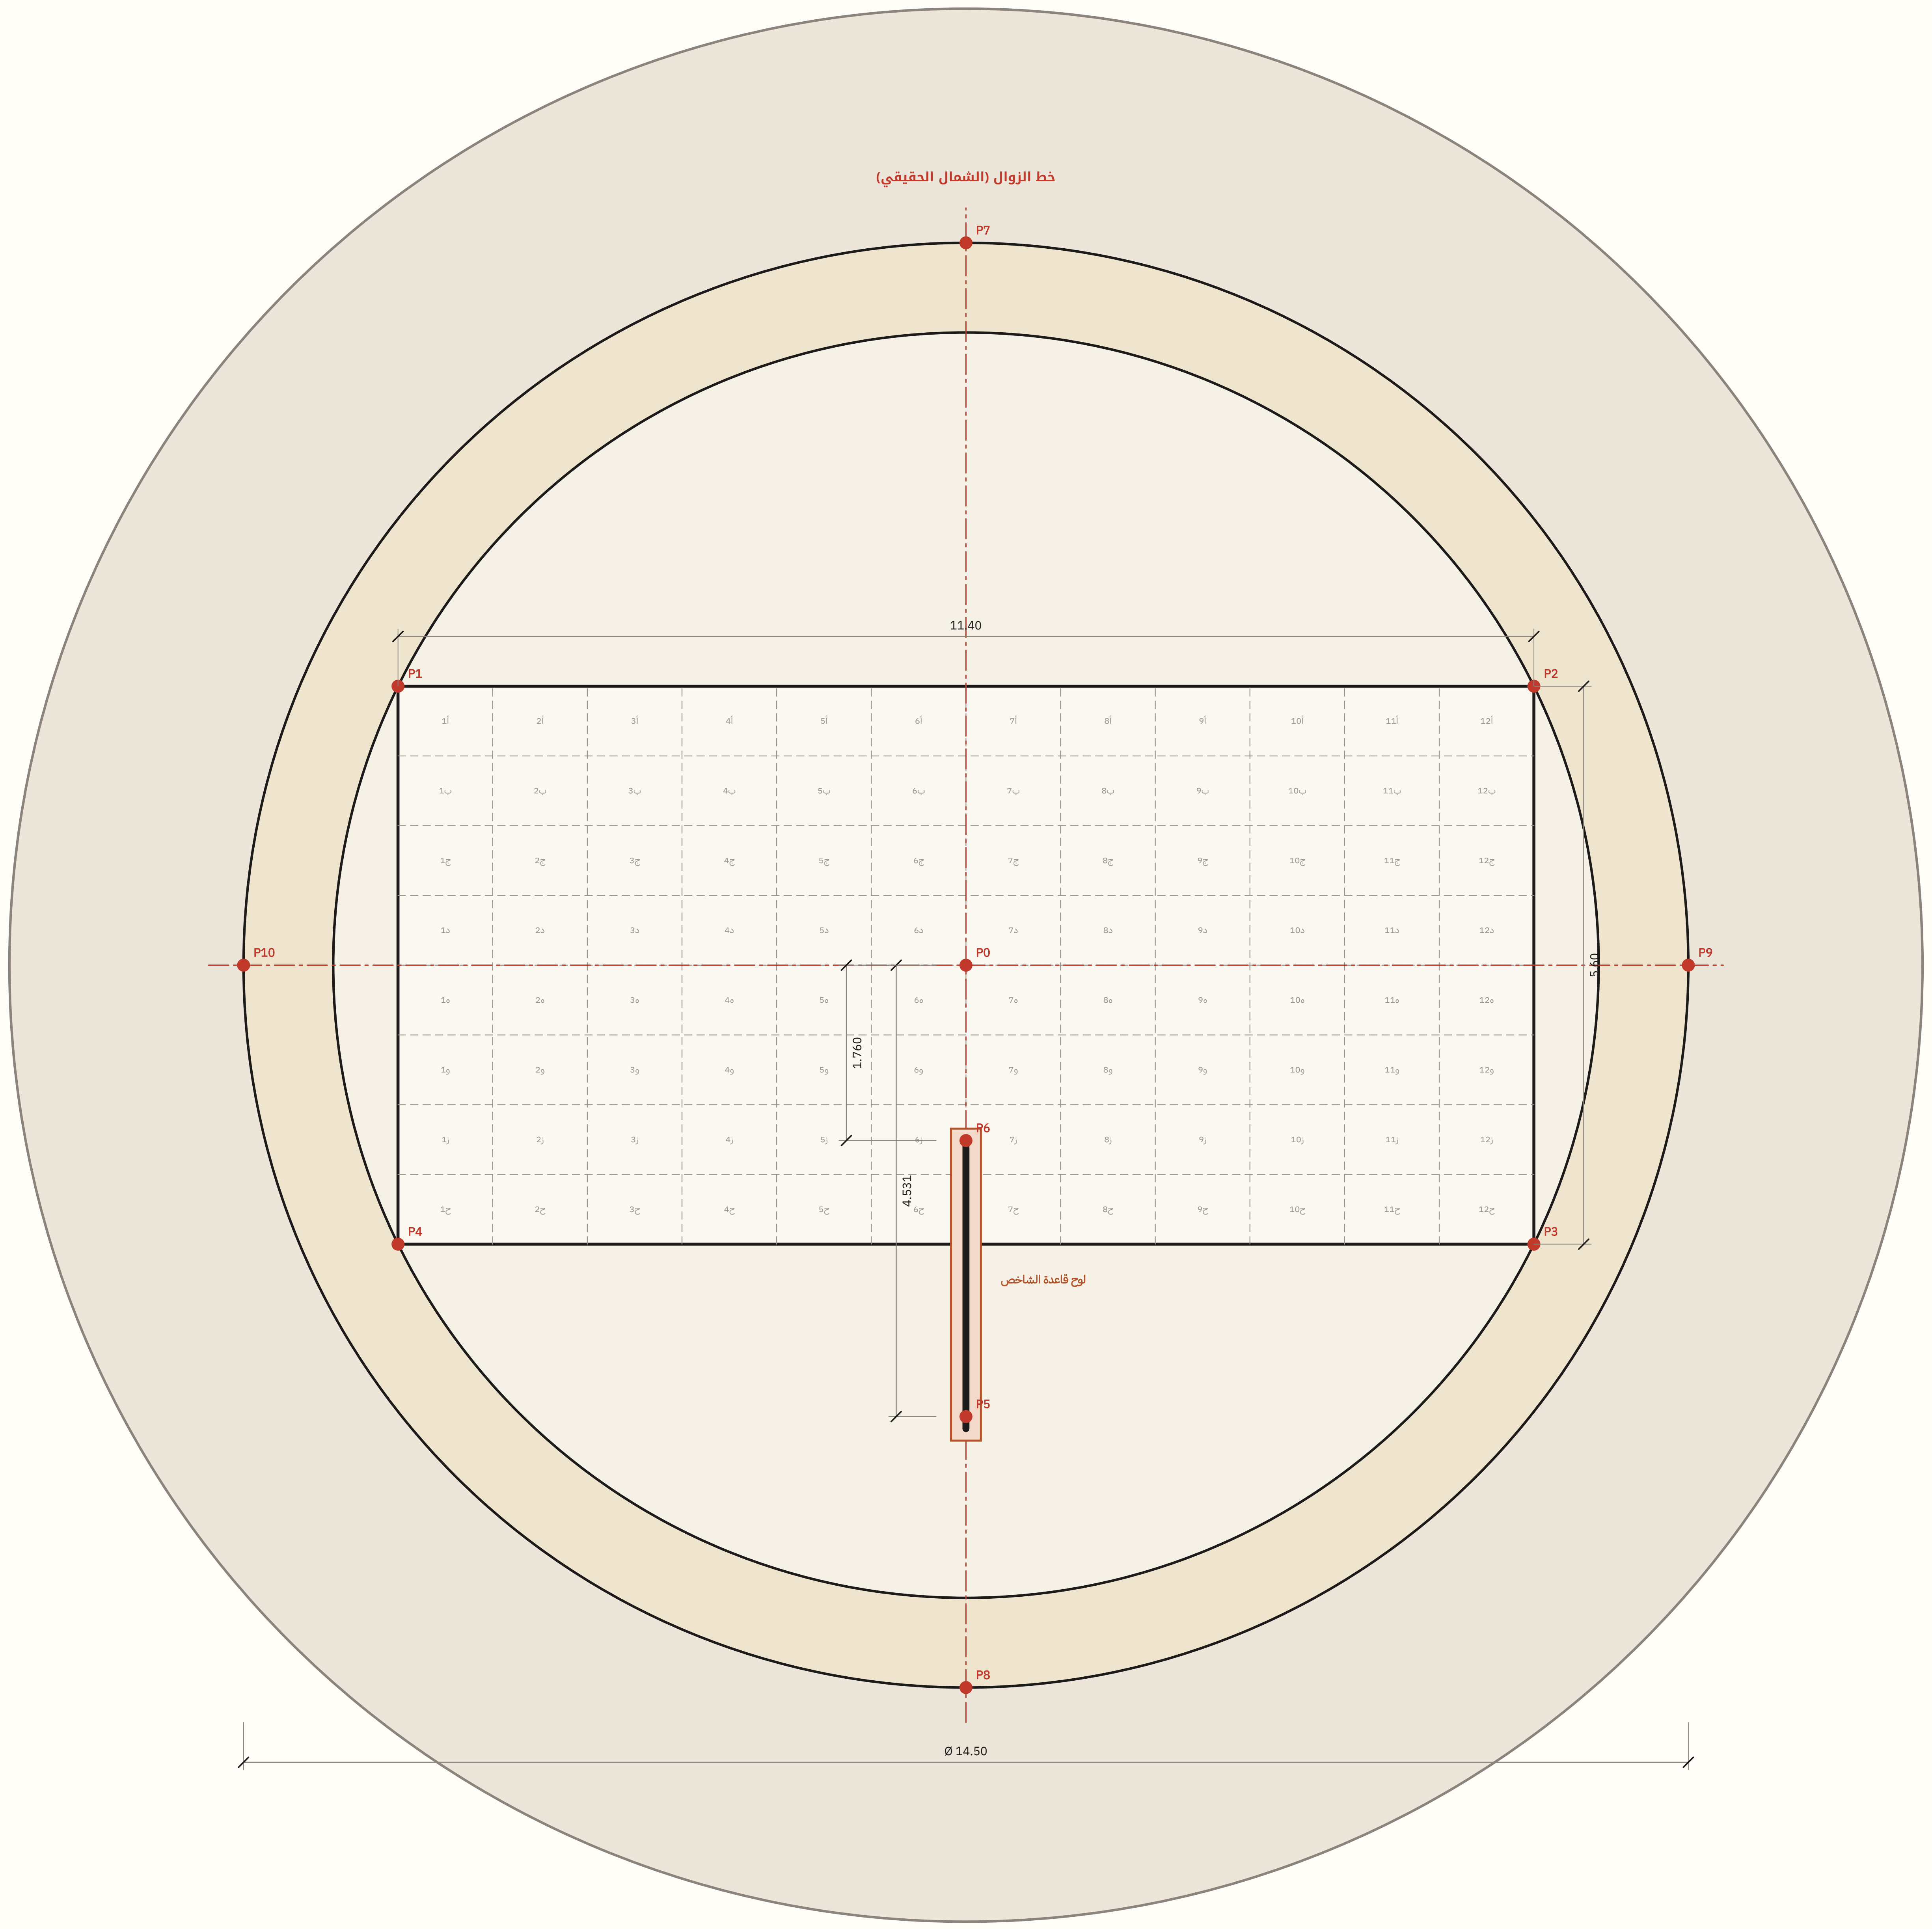
P7
P1
P2
P10
P0
P9
P4
P3
P6
P5
P8
11.40
5.60
1.760
4.531
Ø 14.50
لوح قاعدة الشاخص
أ1 أ2 أ3 أ4 أ5 أ6 أ7 أ8 أ9 أ10 أ11 أ12
ب1 ب2 ب3 ب4 ب5 ب6 ب7 ب8 ب9 ب10 ب11 ب12
ج1 ج2 ج3 ج4 ج5 ج6 ج7 ج8 ج9 ج10 ج11 ج12
د1 د2 د3 د4 د5 د6 د7 د8 د9 د10 د11 د12
ه1 ه2 ه3 ه4 ه5 ه6 ه7 ه8 ه9 ه10 ه11 ه12
و1 و2 و3 و4 و5 و6 و7 و8 و9 و10 و11 و12
ز1 ز2 ز3 ز4 ز5 ز6 ز7 ز8 ز9 ز10 ز11 ز12
ح1 ح2 ح3 ح4 ح5 ح6 ح7 ح8 ح9 ح10 ح11 ح12

النقطة	x (م)	y (م)	E شبكي	N شبكي	الوصف
P0	+0.000	+0.000	638413.300	810602.700	مركز الدائرة
P1	-5.700	+2.800	638407.594	810605.488	ركن الرخامة ش.غ
P2	+5.700	+2.800	638418.994	810605.512	ركن الرخامة ش.ق
P3	+5.700	-2.800	638419.006	810599.912	ركن الرخامة ج.ق
P4	-5.700	-2.800	638407.606	810599.888	ركن الرخامة ج.غ
P5	+0.000	-4.531	638413.310	810598.169	قاعدة الضلع القطبي عند ±0.00
P6	+0.000	-1.760	638413.304	810600.940	مسقط العقدة (ارتفاعها 1.600)
P7	+0.000	+7.250	638413.285	810609.950	طرف خط الزوال شمالًا
P8	+0.000	-7.250	638413.315	810595.450	طرف خط الزوال جنوبًا
P9	+7.250	+0.000	638420.550	810602.715	طرف خط الاعتدال شرقًا
P10	-7.250	+0.000	638406.050	810602.685	طرف خط الاعتدال غربًا

الشمال الحقيقي

الشمال الشبكي منحرف 0.12° شرقًا

الموقع: φ = 30.0054° ش • λ = 31.2443° ق
مركز المزولة (الحزام الأحمر): E 638413.3 • N 810602.7
القطر: 14.50 م
مقياس الرسم: 1:50
التاريخ: أكتوبر 2026
الحالة: مقترح تصميمي للمفاضلة

E-01