مشروع حدائق الفسطاط — المرحلة الثانية

منطقة الحدائق التراثية • البند SF-12: المزولة الشمسية

التصميم (أ): المزولة الجامعة

القطاعات وتفاصيل البناء

قطاع شمال–جنوب في خط الزوال
وتفاصيل الحافة والشاخص والفواصل

ملاحظات

- التربة: إحلال وتسوية ودمك 95% (بروكتور المعدل).
- أساس حصوي متدرج 250 مم مدموك على طبقتين.
- بلاطة خرسانة مسلحة C30 سمك 150 مم، شبكتان Ø10 كل 150 مم، فواصل تمدد عند حلقة 6.35 م فقط؛ لا فواصل تحت الوجه.
- تسوية سطح البلاطة ±3 مم، ومونة لصق 30 مم إيبوكسي/أسمنتية.
- الرخام 40 مم؛ حلقة التقويم جرانيت رمادي 40 مم.
- الحافة جرانيت أحمر أسوان 180 × 300 مم مشطوفة 10 مم.
- الصرف: الوجه أفقي تمامًا؛ تُترك فواصل الحلقة الخارجية مفتوحة 6 مم فوق مجرى خطي خفي 100 مم على المحيط.
- أساس الشاخص: تعميق البلاطة 400 مم أسفل لوح القاعدة بعرض 800 مم وطول 3.6 م، حديد Ø12 كل 150 مم.

الموقع	φ = 30.0054° ش • λ = 31.2443° ق
مركز المزولة (الحزام الأحمر)	E 638413.3 • N 810602.7
القطر	14.50 م
مقياس الرسم	1:30 و1:5
التاريخ	أكتوبر 2026
الحالة	مقترح تصميمي للمفاضلة

E-03

القطاع أ–أ: في خط الزوال (الشمال يمينًا) — 1:30

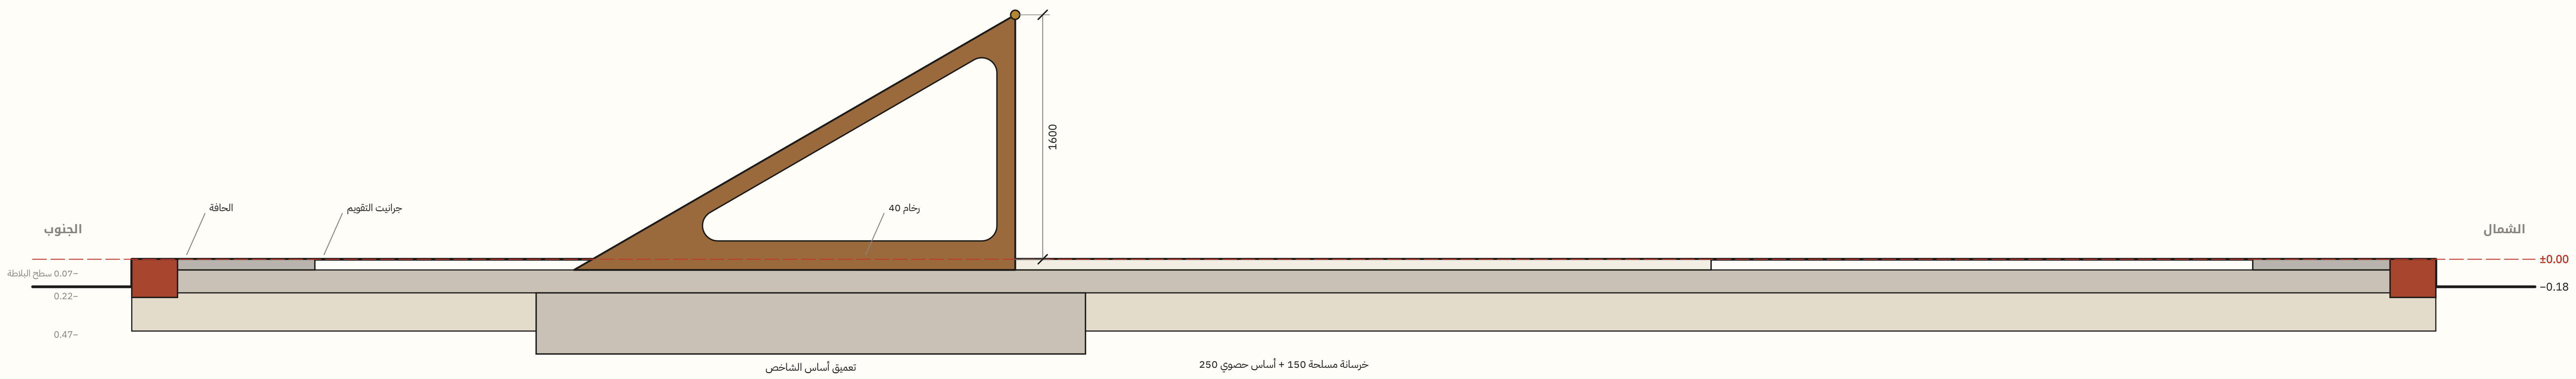

ت1: قاعدة ا اخص — 1:5

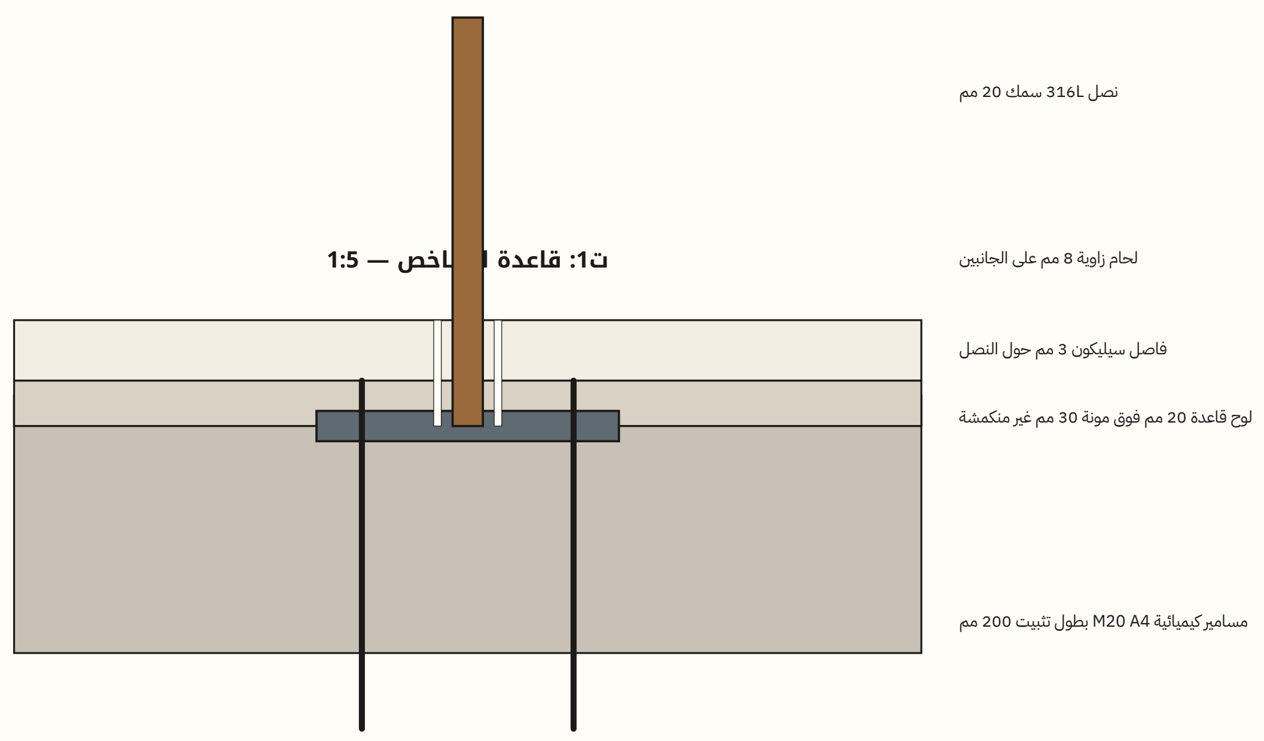
نصل 316L سمك 20 مم
لحام زاوية 8 مم على الجانبين
فاصل سيليكون 3 مم حول النصل
لوح قاعدة 20 مم فوق مونة 30 مم غير منكمشة
مسامير كيميائية M20 A4 بطول تثبيت 200 مم

ت3: الحافة والصرف المحيطي — 1:5

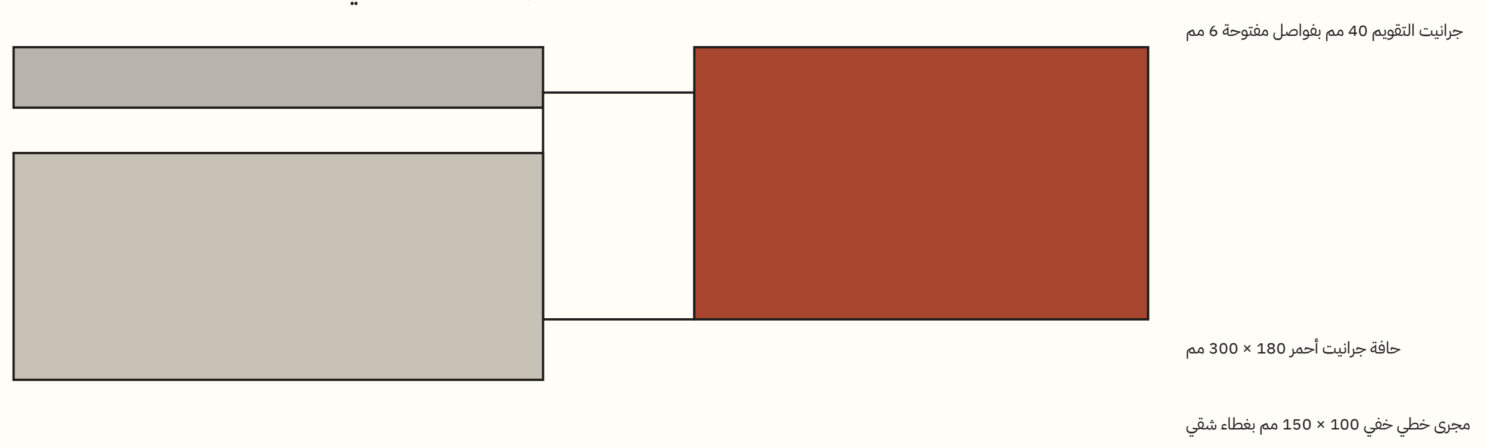
جرانيت التقويم 40 مم بفواصل مفتوحة 6 مم
حافة جرانيت أحمر 180 × 300 مم
مجرى خطي خفي 100 × 150 مم بغطاء شقي

ت2: فاصل الألواح والتطعيم — 1:5

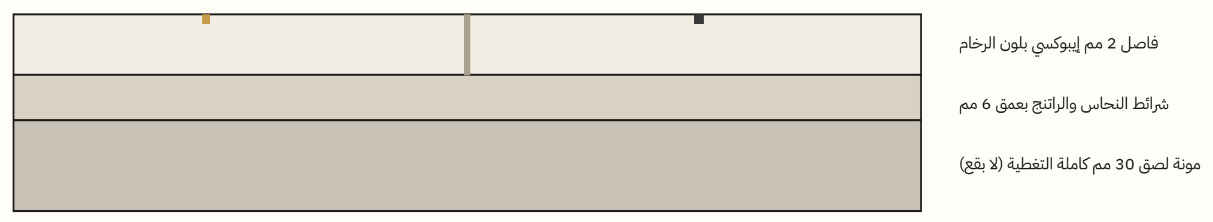
فاصل 2 مم إيبوكسي بلون الرخام
شرائط النحاس والراتنج بعمق 6 مم
مونة لصق 30 مم كاملة التغطية (لا بقع)