

التصميم (ج): بوابة عين الشمس


البوابة: واجهة وقطاع الزوال وتفاصيل الثقب

قوس فاطمي «مكتبر» على هيئة عقود الجامع الأقمر
يحمل قرص الشمس المثقوب


ملاحظات

- الدعائم والقنب: حجر جيري (مائلة) على هيكل خرساني.
- الشمس: قرص برونز 1.20 م سمك 12 مم مائل 30° عن الأفق (عمودي على شعاع ظهر الاعتدال) لنقل زاوية سقوط الضوء.
- القنب: 50 مم بواجهة مسطوفة 45° من الجهة السفلية.
- قمة البوابة (3.85 م) تحت مستوى القنب حتى لا تعجب الشمس.
- البوابة داخل الساحة يمر بها الزوار، وعلمتها خارج مسار البوابة.
- التكلفة الكلية في الإبريق (الشمس والقنبر بحدائق).
- تقاوت موضع القنب: 54 مم أعلى و35 مم رأسياً.
- منحى معادلة الزمن مقفول على الدعامة الشرقية للتعليم.


الواجهة الجنوبية للبوابة — 1:25

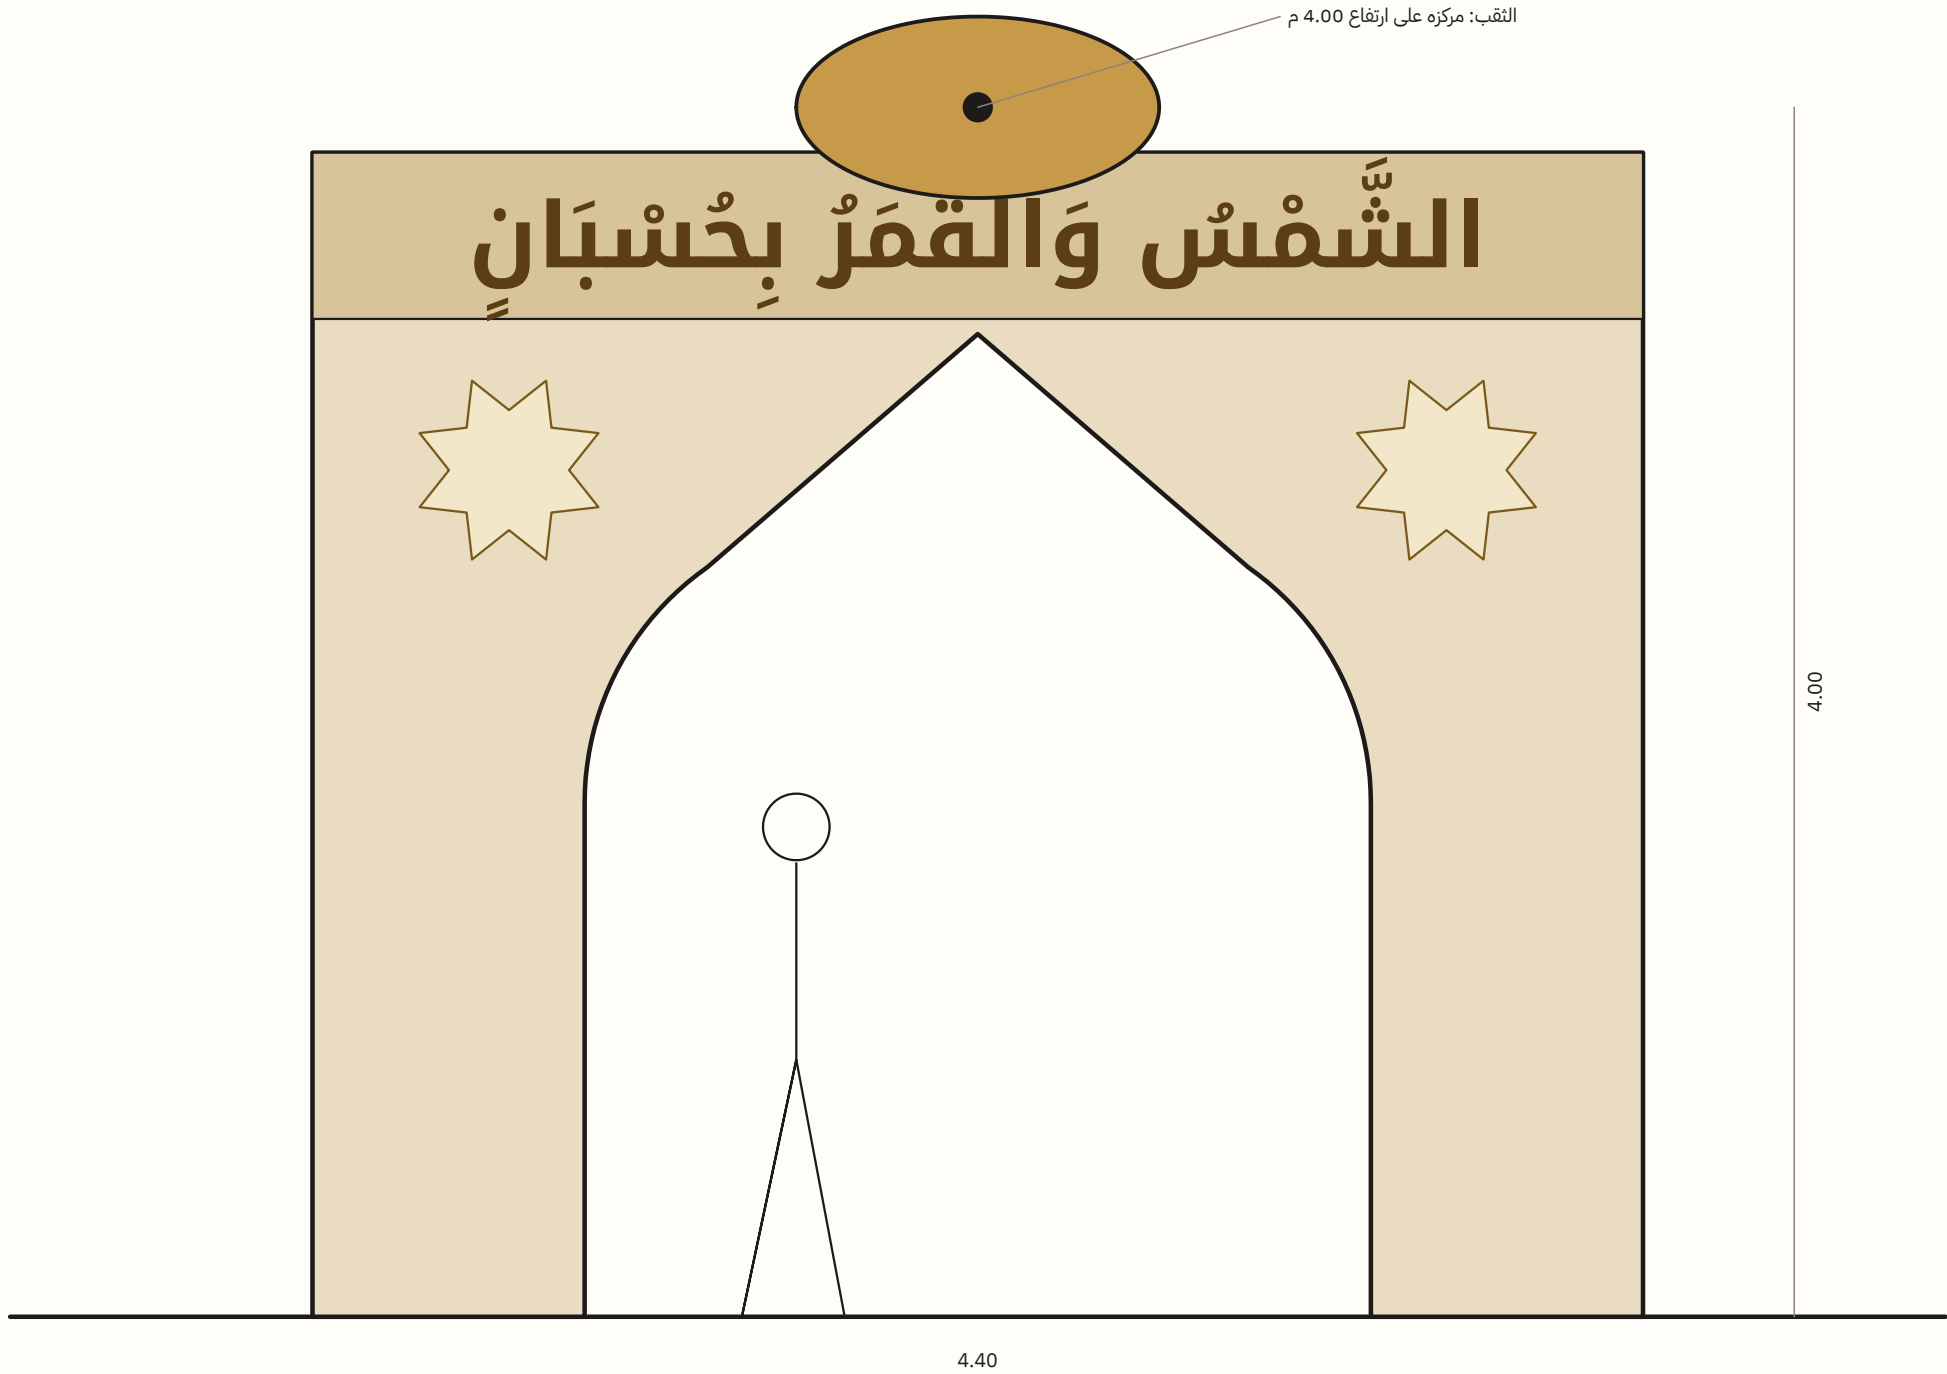


قطاع الزوال (شمال-جنوب) — 1:50: أشعة الظهر

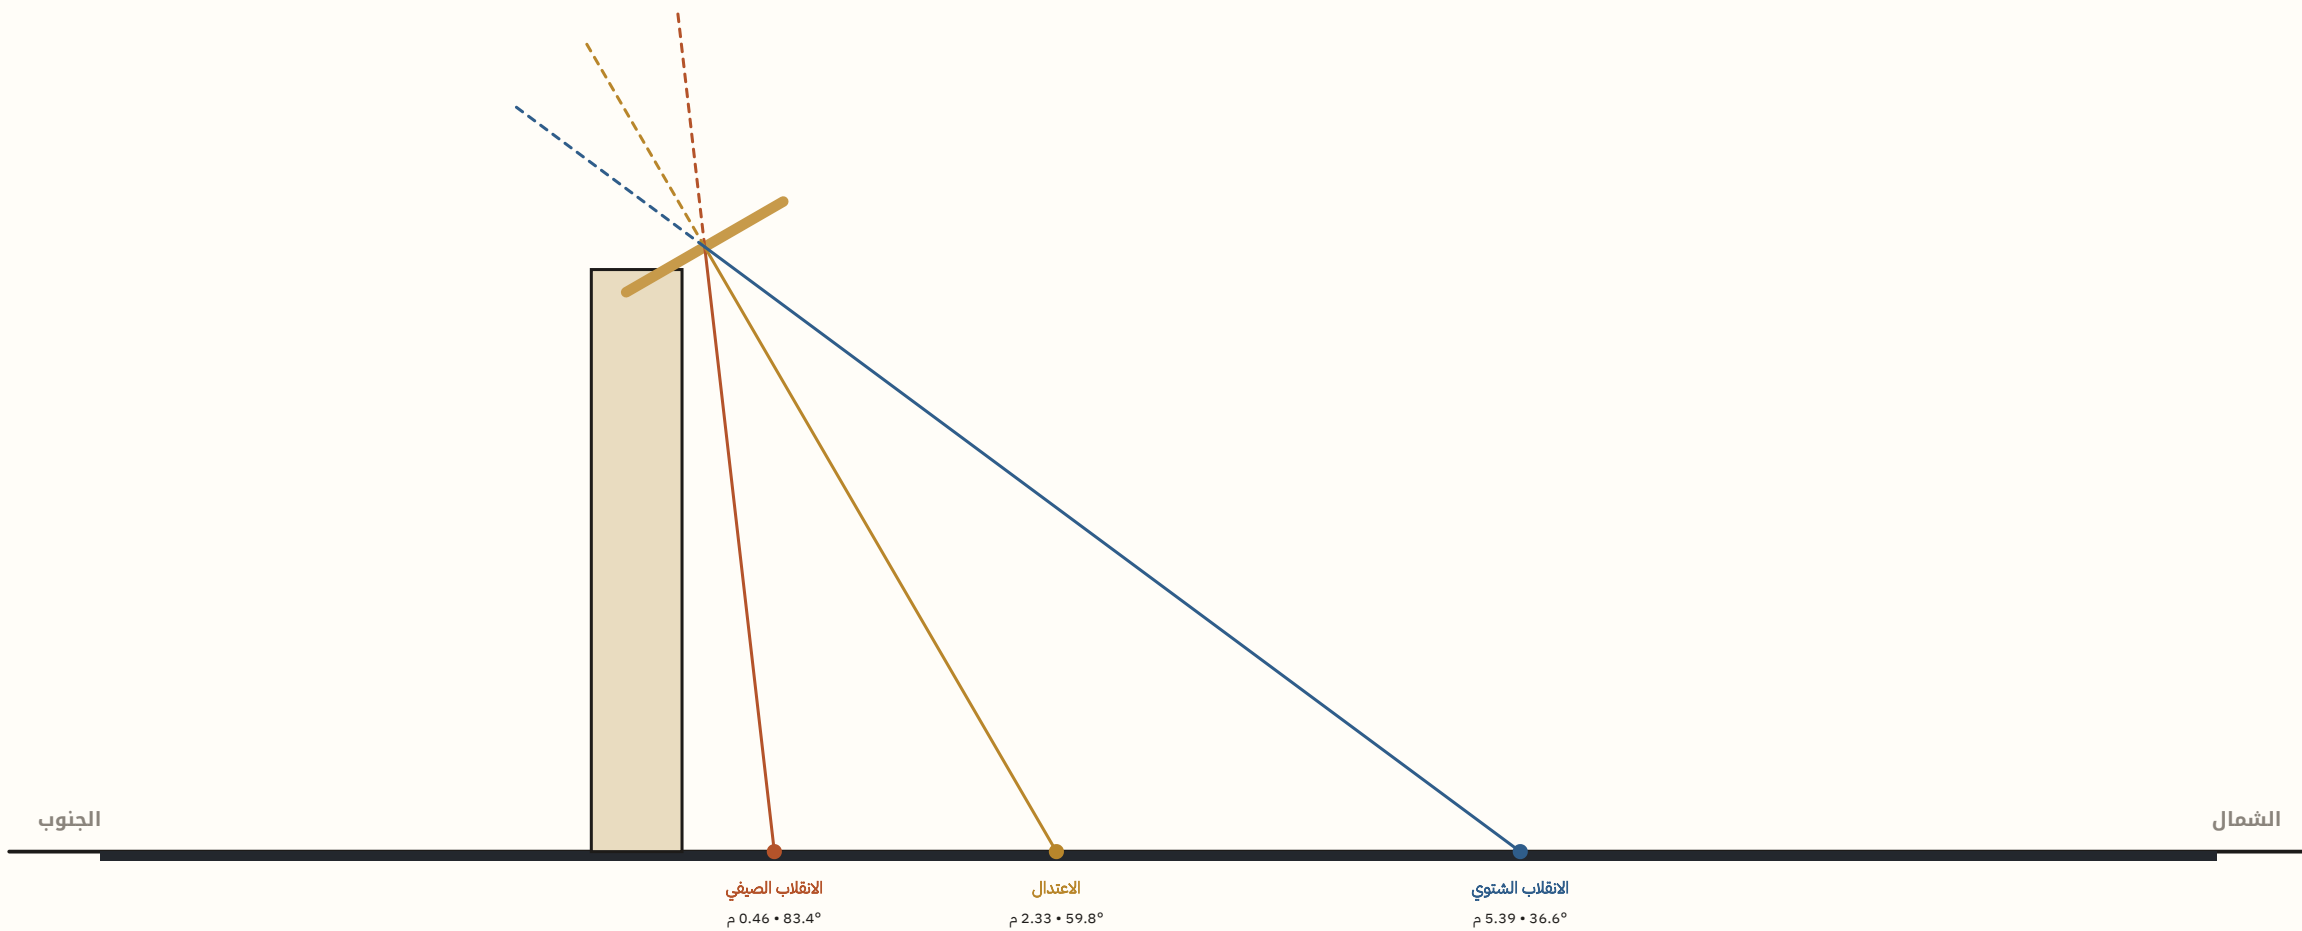

تفصيل الشمس والقنب — 1:10 (مسقط عمودي على القرص)

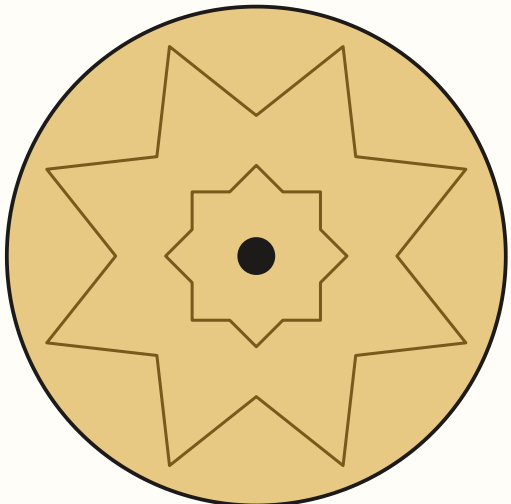

معادلة الزمن: ما يُضاف إلى قراءة الموزلة (حدائق)

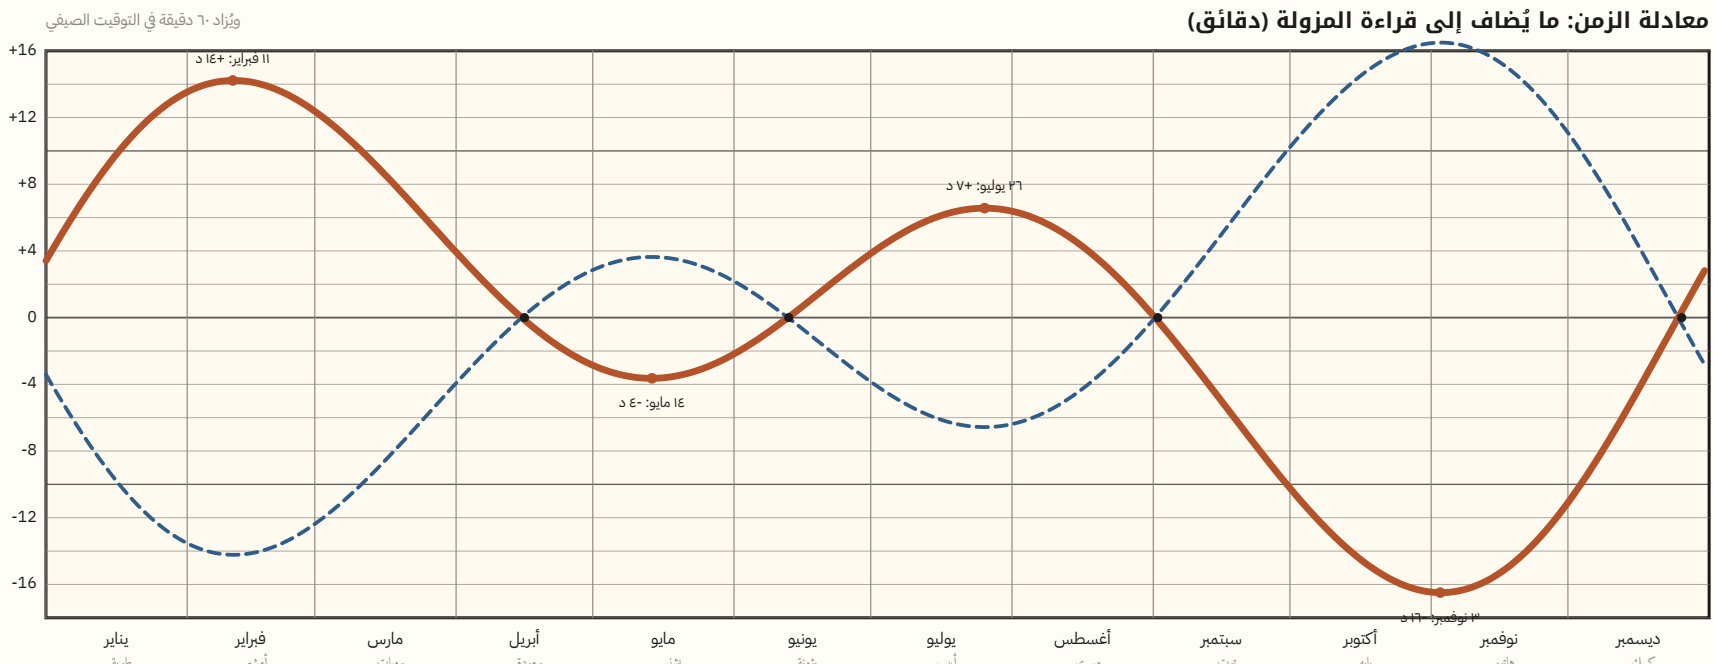

المنطق الأقرب: معادلة الزمن نفسها (الوقت الشمسي - الوقت المتوسط) = للتعليم

الموقع

في 31.2443° شمال و 30.0054° شرق

مركز الموزلة (الحزام الأحمر)

E 638413.3 • N 810602.7

القطر

م 14.50

مقياس الرسم

(A1 على لوح) و 1:50 و 1:10 و 1:25

التاريخ

أكتوبر 2026

الحالة

مقترح تصميمي للمفاضلة

C-02