

## مشروع حدائق الفسطاط – المرحلة الثانية

منطقة الحدائق التراثية • البند SF-12: المزالة الشمسية

### التصميم (د): رخامة ابن الصوفي

## المسقط العام والواجهات

قرص مواز لمعدل النهار مائل 60° عن الأفق

محموله دعامتان حجریتان شرقاً و غرباً

### ملاحظات

• مأخوذ من «صناعة الرخامة الموازية لمعدل النهار» في

مخطوط شفاء الأسقام في وضع الساعات على الرخام

لشهاب الدين أحمد بن الصوفي (لوحة M-01).

• **القرص:** قطر 3.60 م، مركزه على ارتفاع 2.00 م فوق مركز الساحة.

مستواه عمودي على المحور القطبي (يميل  $59.9946^\circ$  عن الأفق).

• الوجه العلوي «الصيفي» يضاء من الاعتدال الربيعي إلى الخريف،  
والسفل «الشتوي» في النصف الآخر من السنة.

• المجدد القطن، زجاجة، قطره 50 مل، وعاء خيزران، علبة 350 مل.


من الوجهين: ظليهما على دوائر البروج يدل على التاريخ.

• ساعات القرص متساوية 15° كما في المخطوط، مزاحة بفرق الطول.


• يوم الاعتدال تكون الشمس في مستوى القرص فلا يضاء وجهه منهما.

• أرضية الساحة: نجمة ثمانية كبرى من الحجر الجيري والبازلت


وحلقة التقويم ولوحا معادلة الزمن ورأس السنة الهجرية.

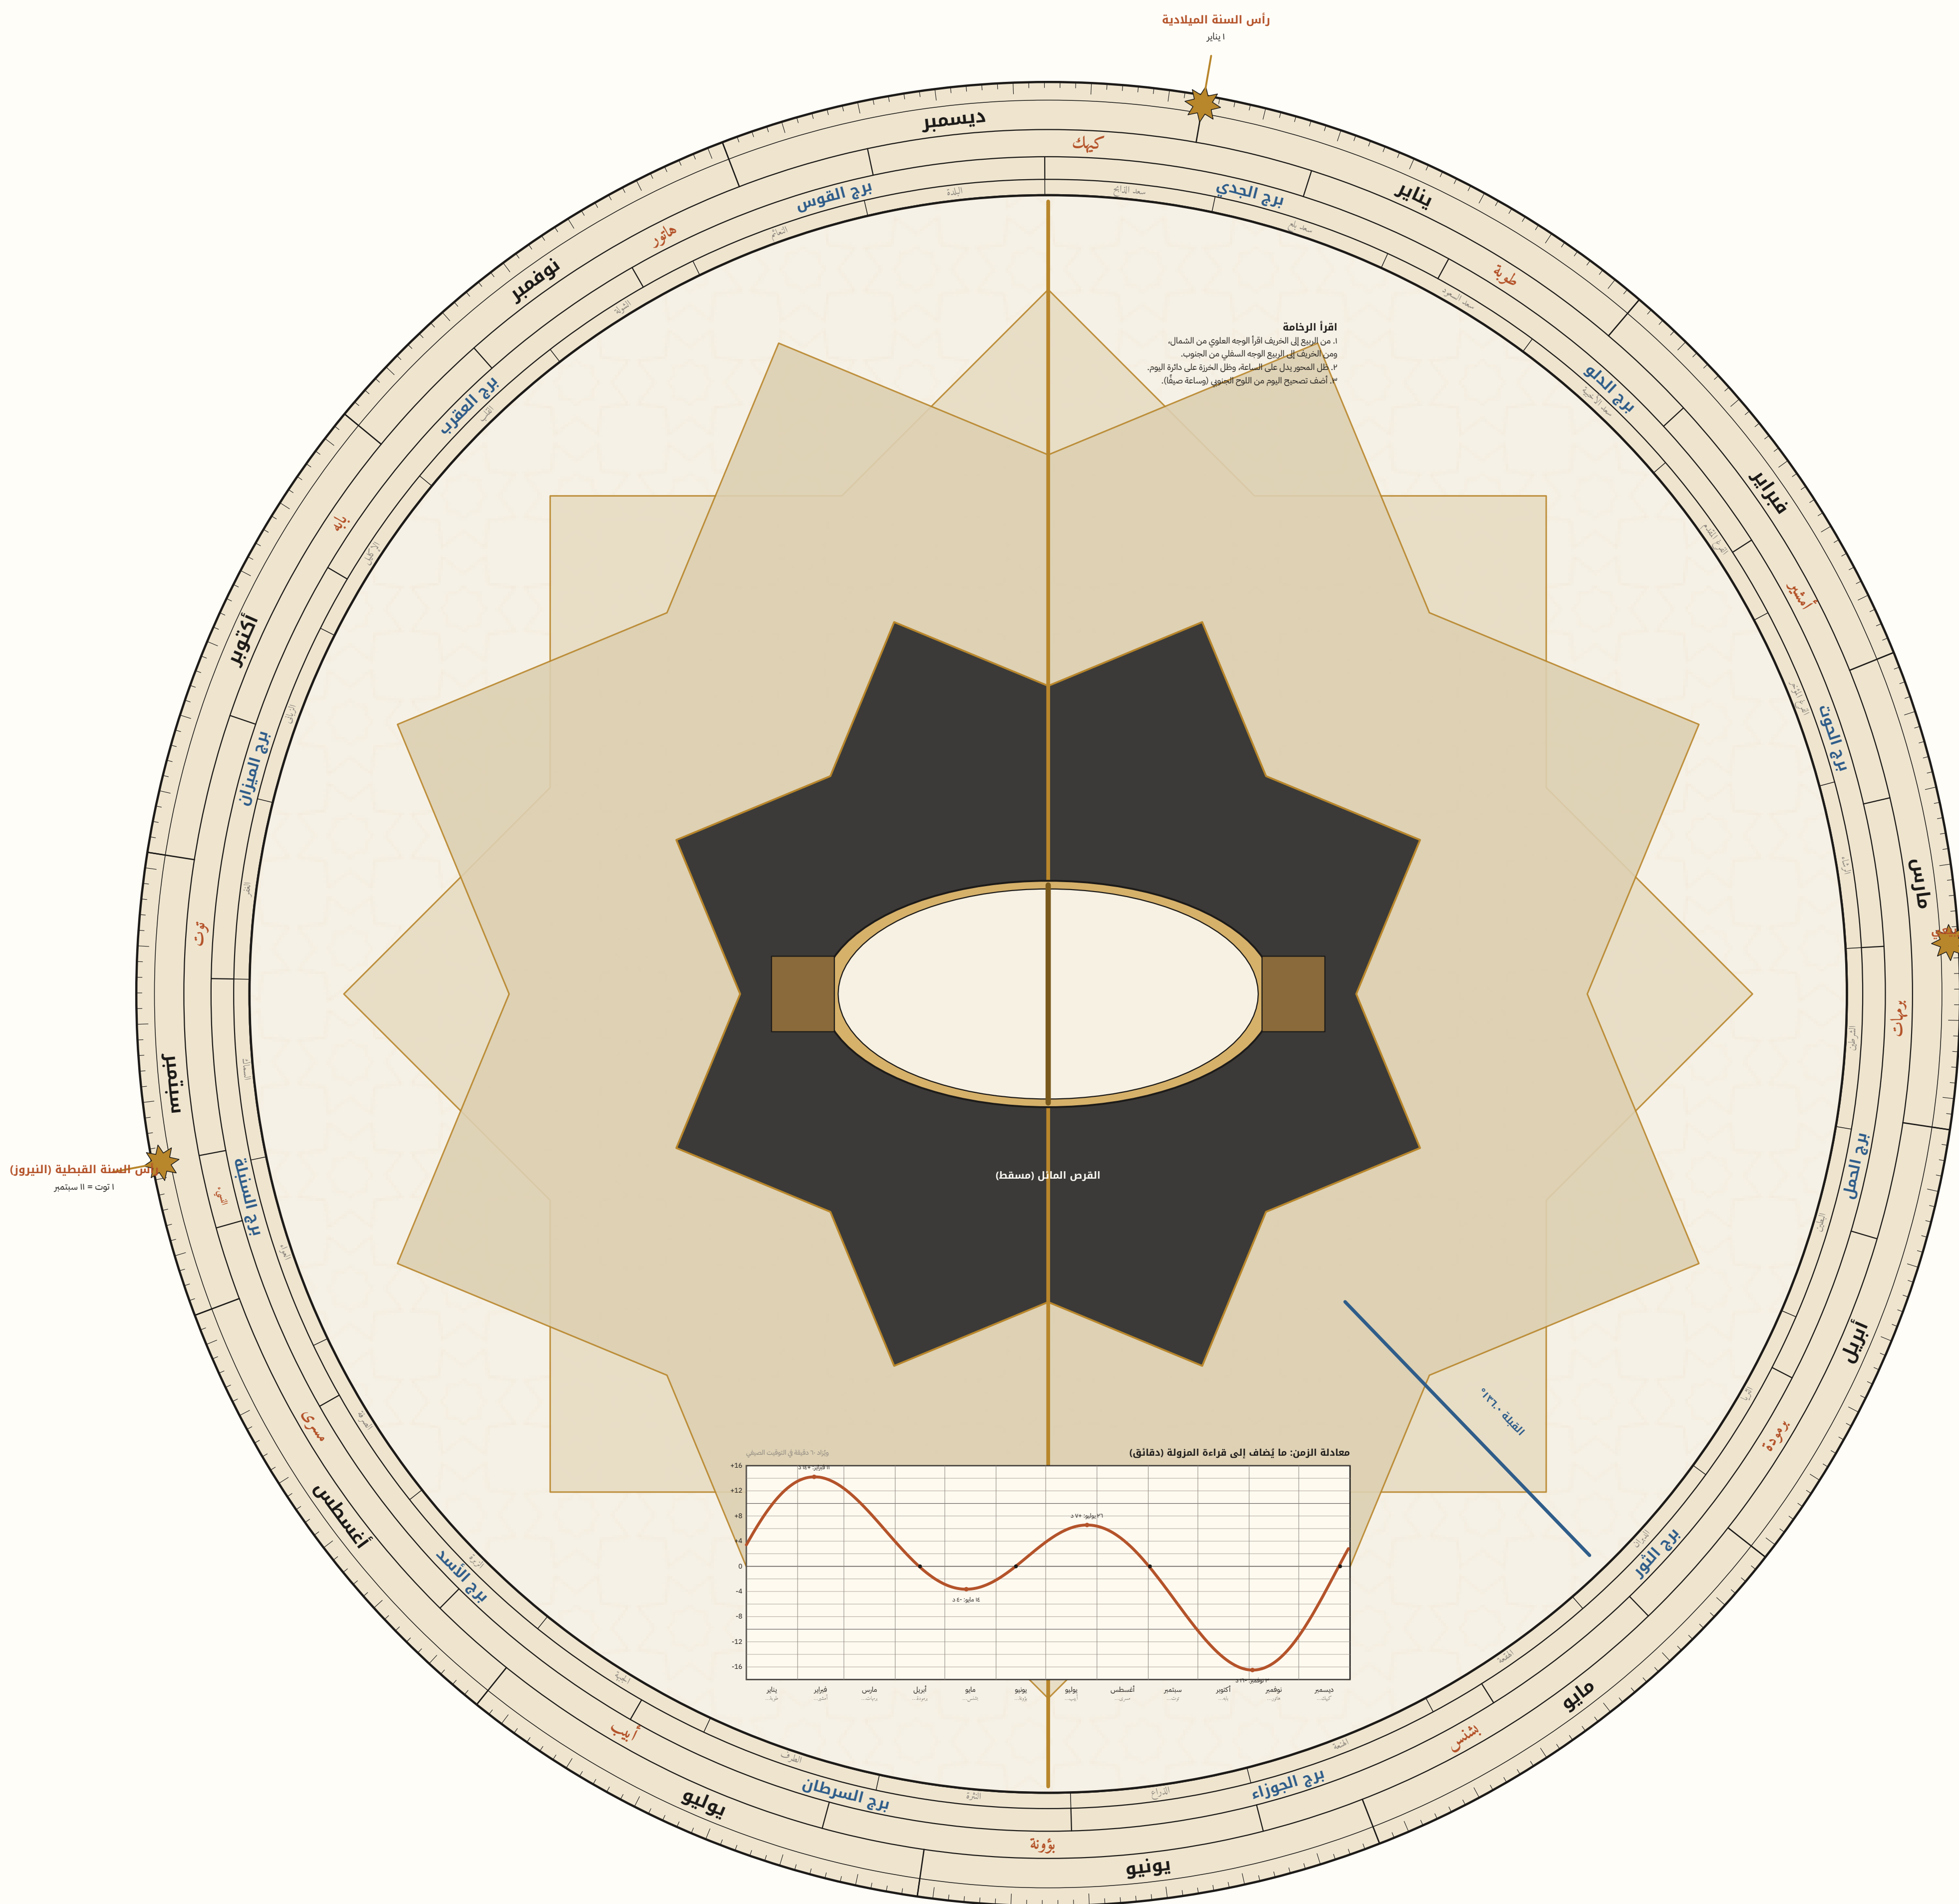

الواجهة الجنوبية — 1:50

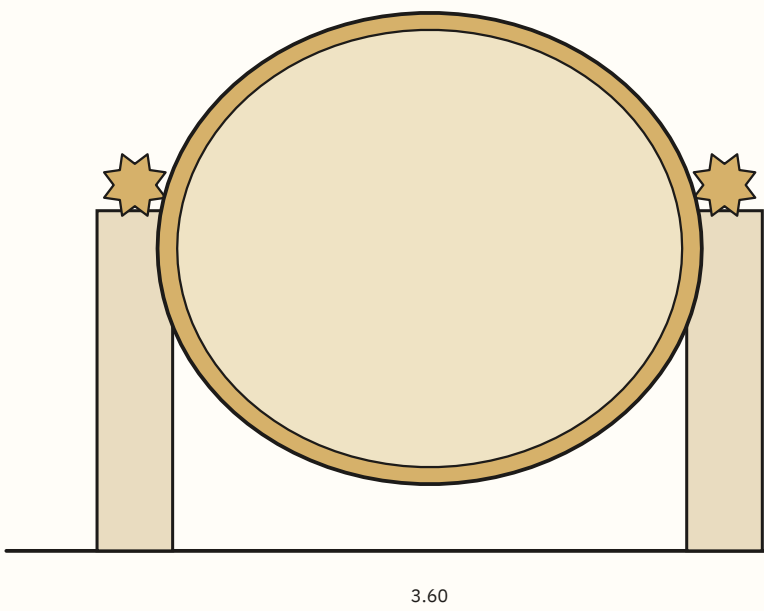

قطاع شمال-جنوب — 1:50 (الشمال يميناً)

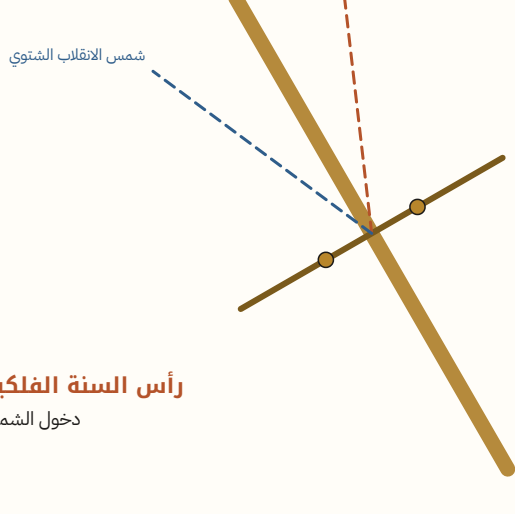

**أس السنة الفلكية: الاعتدال الربيعي**  
دخول الشمس برج الحمل

دخول الشمس برج الحمل

الجنوب

القرص يميل  $59.99^\circ$  عن الأفق، والمحور  $30.01^\circ$  نحو القطب

## الشمال الحقيقي



الشمال الشبكي منحرف  $0.12^\circ$  شرقاً



الموقع

مركز المزولة (الحزام الأحمر)

القطر

### مقياس الرسم

## التاريخ

## الحالة

D-01