## مشروع حدائق الفسطاط — المرحلة الثانية

منطقة الحدائق التراثية • البند SF-12: المزولة الشمسية

---

# التصميم (أ): مزولة الشاخص القطبي

## تقسيم بلاط الوجه وحلقة التقويم

172 بلاطة رخام و36 قطاع جرانيت
لكل قطعة رقم وملف قص

---

### ملاحظات

- البلاط 900 × 900 × 40 مم؛ الأعمدة A… من الغرب، والصفوف من الشمال.
- 108 بلاطة كاملة و64 بلاطة مقصوصة بالدائرة أو بشق النصل.
- كل بلاطة تُقص وتُحفر في المصنع من ملفها: dxf/tiles/<الرقم>.dxf (الأصل ركنها الجنوبي الغربي، الوحدة مم)، ويُكتب رقمها على ظهرها.
- شق النصل: 40 مم على خط الزوال من P5−20 إلى P6+20 مم.
- قطاعات الحلقة 36 × 10° من الشمال باتجاه عقارب الساعة (R01…R36).
- الفواصل 2 مم إيبوكسي بلون الحجر؛ لا فواصل تمدد داخل الوجه.
- ضُمت 8 شرائح صغيرة عند أطراف المحورين إلى جاراتها (900 × 950).
- تفصيل كل قطعة وحفرها في جدول القطع X-08.

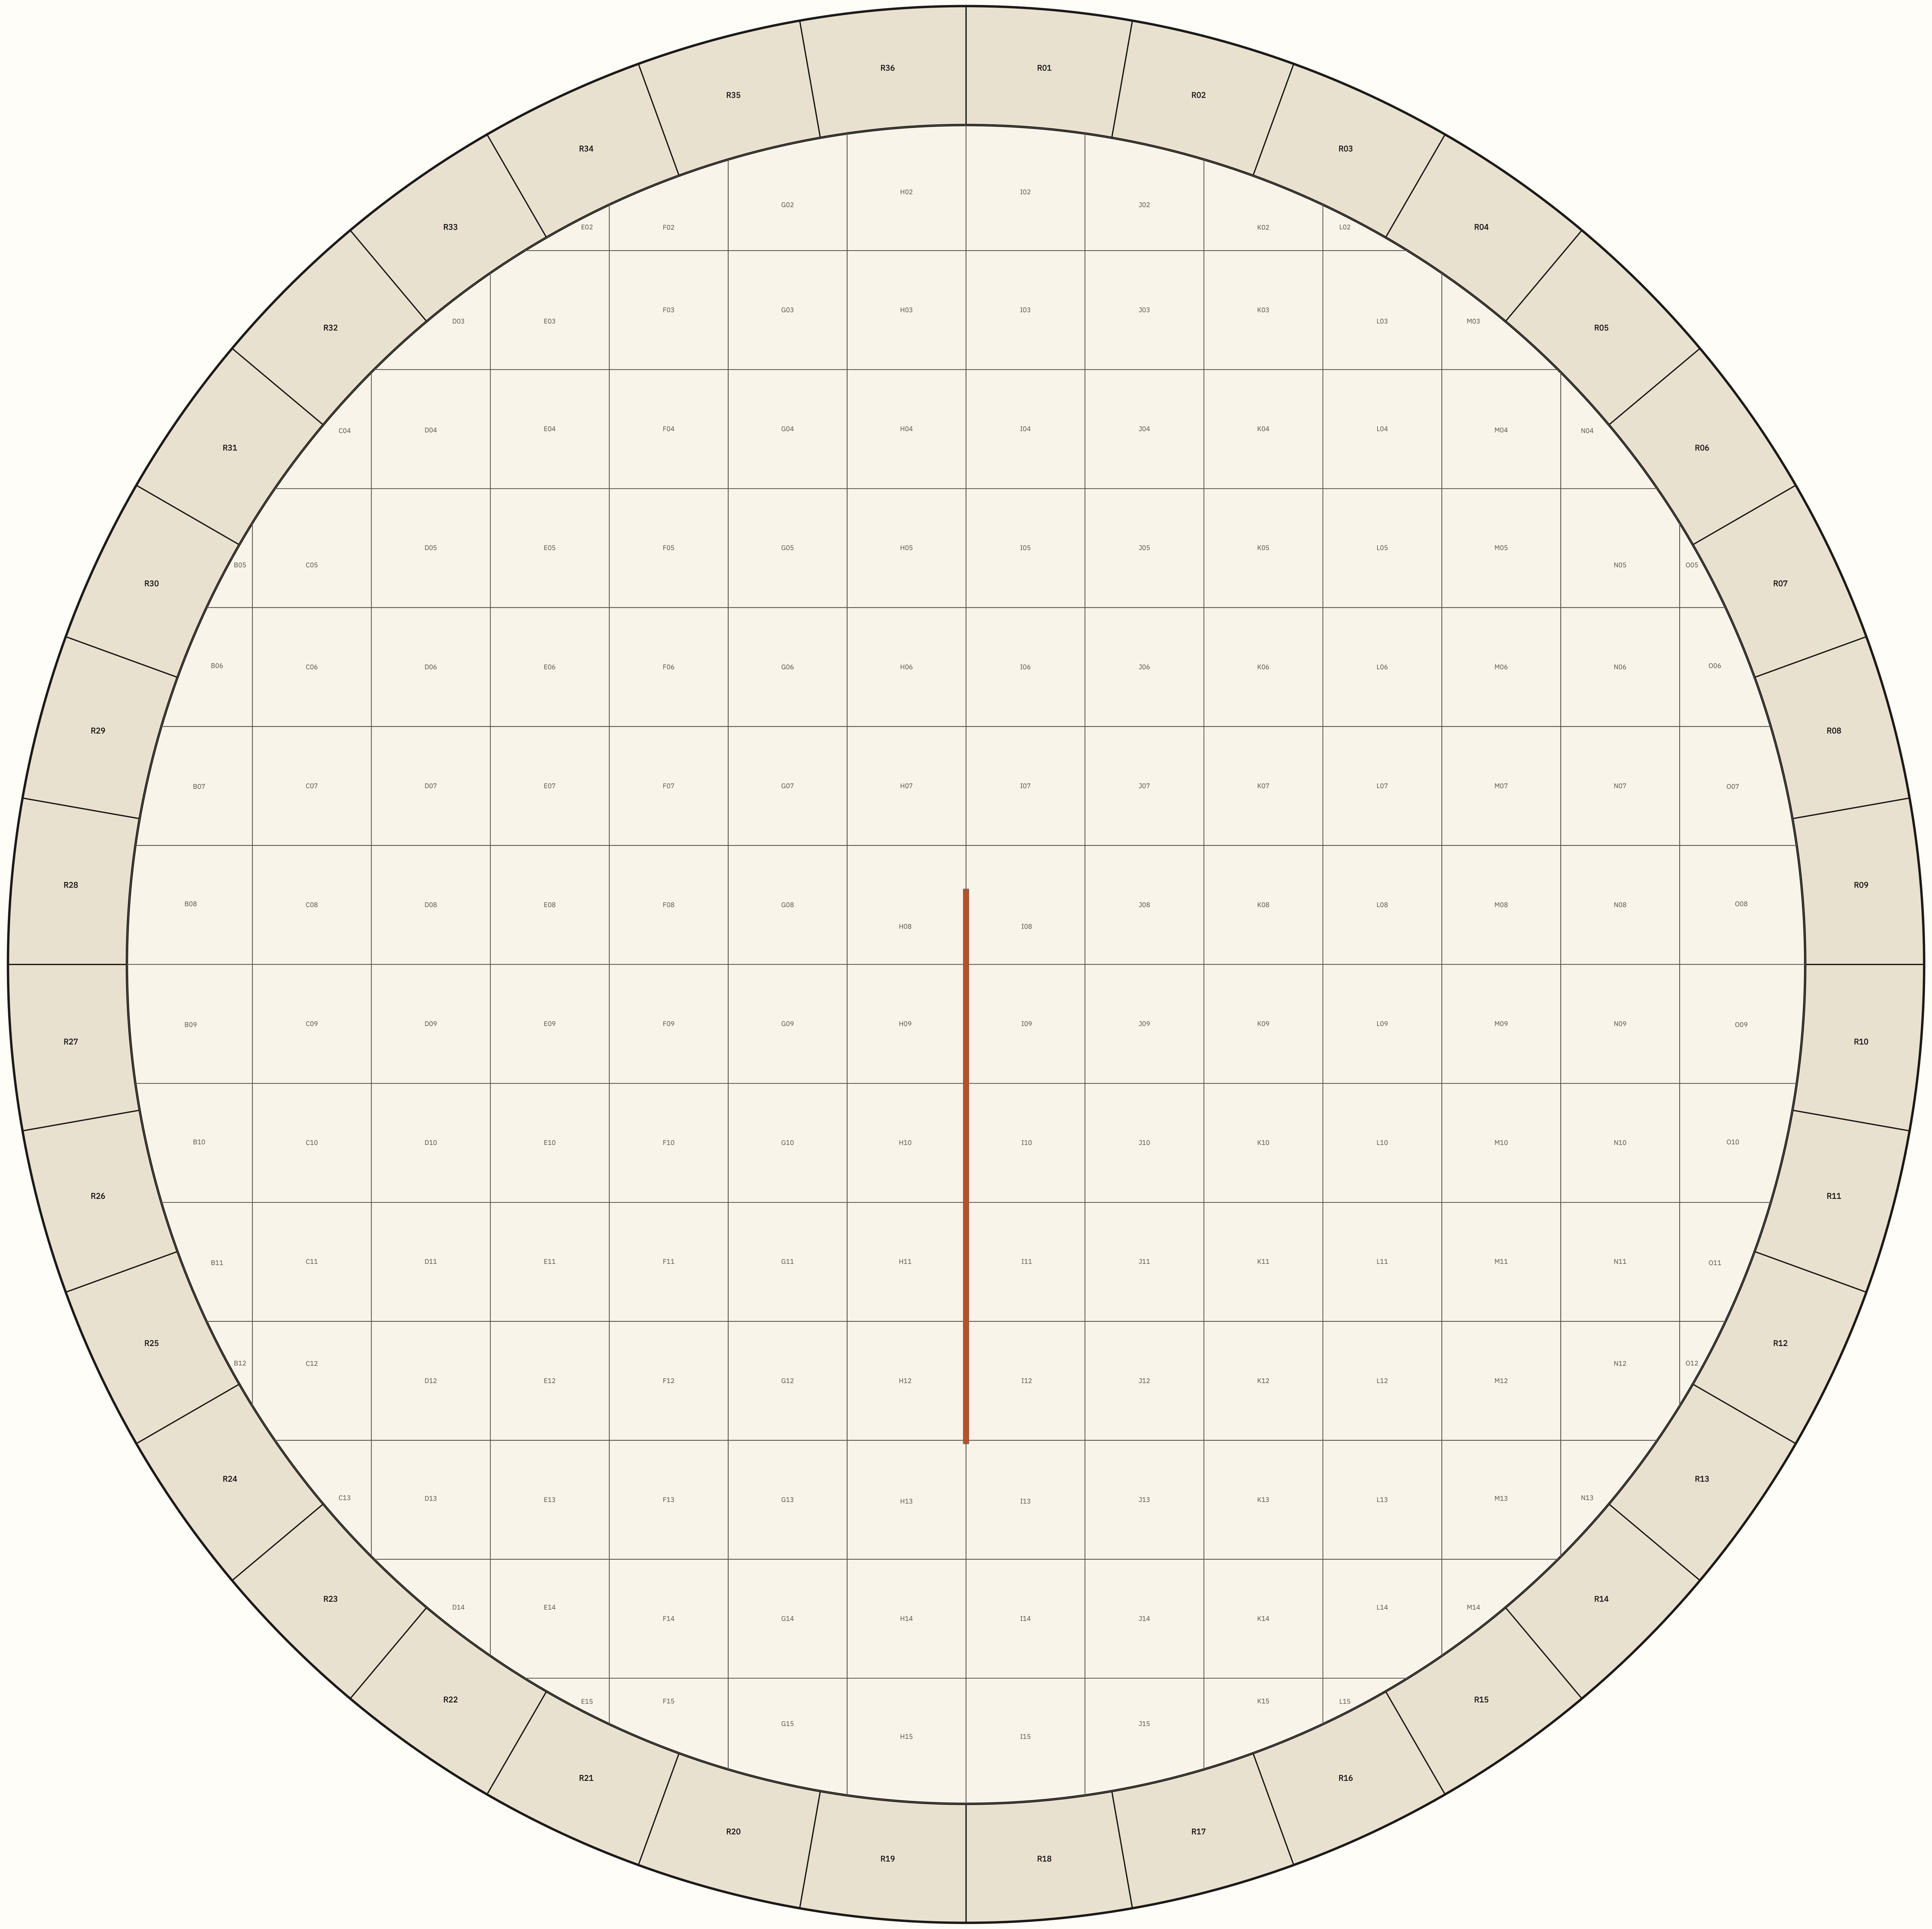
R01
R02
R03
R04
R05
R06
R07
R08
R09
R10
R11
R12
R13
R14
R15
R16
R17
R18
R19
R20
R21
R22
R23
R24
R25
R26
R27
R28
R29
R30
R31
R32
R33
R34
R35
R36
E02 F02 G02 H02 I02 J02 K02 L02
D03 E03 F03 G03 H03 I03 J03 K03 L03 M03
C04 D04 E04 F04 G04 H04 I04 J04 K04 L04 M04 N04
B05 C05 D05 E05 F05 G05 H05 I05 J05 K05 L05 M05 N05 O05
B06 C06 D06 E06 F06 G06 H06 I06 J06 K06 L06 M06 N06 O06
B07 C07 D07 E07 F07 G07 H07 I07 J07 K07 L07 M07 N07 O07
B08 C08 D08 E08 F08 G08 H08 I08 J08 K08 L08 M08 N08 O08
B09 C09 D09 E09 F09 G09 H09 I09 J09 K09 L09 M09 N09 O09
B10 C10 D10 E10 F10 G10 H10 I10 J10 K10 L10 M10 N10 O10
B11 C11 D11 E11 F11 G11 H11 I11 J11 K11 L11 M11 N11 O11
B12 C12 D12 E12 F12 G12 H12 I12 J12 K12 L12 M12 N12 O12
C13 D13 E13 F13 G13 H13 I13 J13 K13 L13 M13 N13
D14 E14 F14 G14 H14 I14 J14 K14 L14 M14
E15 F15 G15 H15 I15 J15 K15 L15

### ملخص الكميات

| البند | الكمية |
|---|---|
| بلاط الوجه (صافي) | 126.5 م² |
| عدد البلاطات | 172 |
| قطاعات الحلقة | 36 (38.5 م²) |
| طول الحافة | 45.6 م |
| هالك مقترح للرخام | 12% |

**الشمال الحقيقي**

الشمال الشبكي منحرف 0.12° شرقًا

0 1 2 3 م

| | |
|---|---|
| الموقع | φ = 30.0054° ش • λ = 31.2443° ق |
| مركز المزولة (الحزام الأحمر) | E 638413.3 • N 810602.7 |
| القطر | 14.50 م |
| مقياس الرسم | 1:30 |
| التاريخ | أكتوبر 2026 |
| الحالة | مقترح تصميمي للمفاضلة |

**X-02**