مشروع حدائق الفسطاط — المرحلة الثانية

منطقة الحدائق التراثية • البند SF-12: المزولة الشمسية

التصميم (أ): مزولة الشاخص القطبي

القطاعات وتفاصيل البناء والأساس

قطاع في خط الزوال، وتفاصيل البلاط والحافة
وأساس الشاخص

ملاحظات

- تربة: إحلال ودمك 95% بروكتور معدل؛ تجربة دمك كل 50 م².
- أساس حصوي متدرج 250 مم على طبقتين.
- بلاطة خرسانة مسلحة C30 سمك 150 مم، شبكتان Ø10 كل 150 مم.
- قاعدة الشاخص: شريط خرساني 5.0 × 1.0 × 0.6 م (C30)، حديد Ø16 كل 150 مم سفلي وعلوي، متصل بالبلاطة.
- لوح القاعدة 30 مم على صواميل ضبط ومونة غير منكمشة 30 مم؛ سطحه العلوي −0.10؛ 12 مسمارًا كيميائيًّا M24 A4 تثبيت 250 مم.
- التشطيب: مونة لصق 30 مم + رخام 40 مم = 70 مم فوق البلاطة.
- الصرف: فواصل الحلقة الخارجية مفتوحة 6 مم فوق مجرى خطي محيطي 100 مم يصب في شبكة الحديقة.
- القيم الإنشائية مقترحة وتُراجع من مهندس إنشائي.

الموقع	φ = 30.0054° ش • λ = 31.2443° ق
مركز المزولة (الحزام الأحمر)	E 638413.3 • N 810602.7
القطر	14.50 م
مقياس الرسم	1:30 و1:5 و1:20
التاريخ	أكتوبر 2026
الحالة	مقترح تصميمي للمفاضلة

X-04

القطاع أ–أ في خط الزوال (الشمال يمينًا) — 1:30

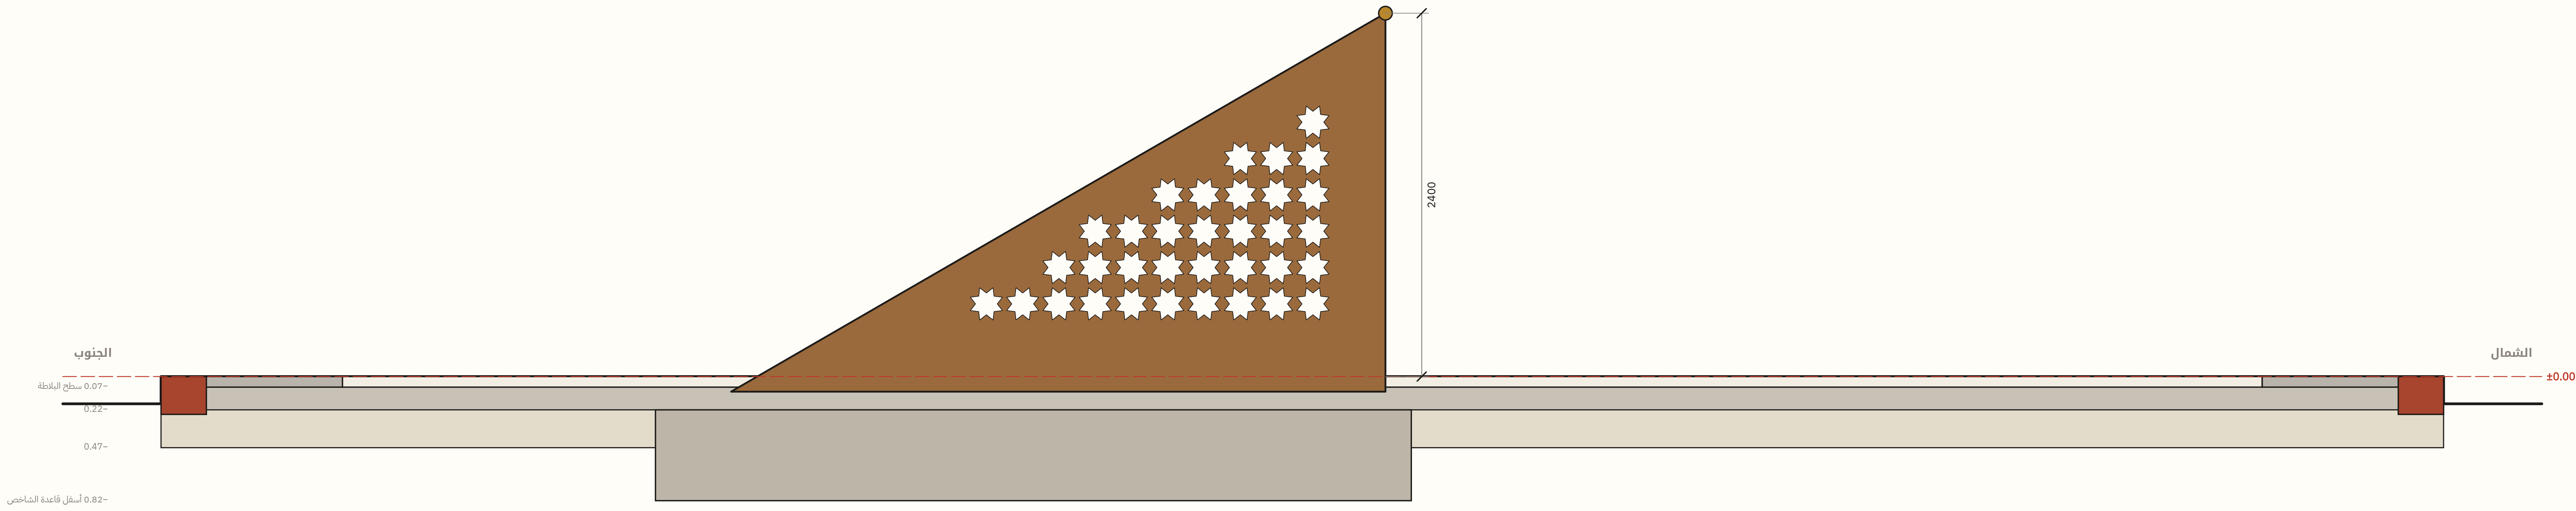

مسقط أساس الشاخص ولوح القاعدة — 1:20 (الشمال يمينًا)

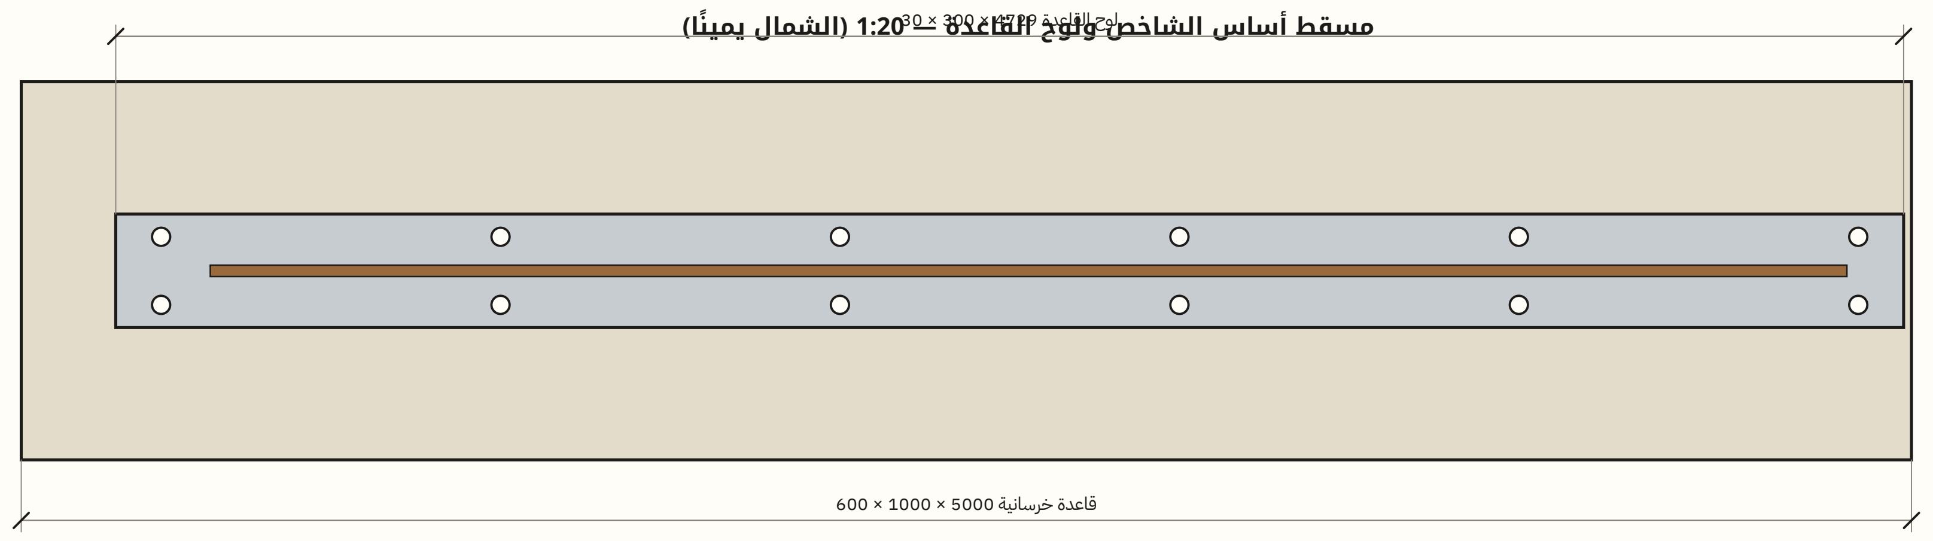

12 مسمار M24 على خطين بينهما 180 مم، خطوة 898 مم — تُصب بقالب ثقب من ملف DXF

ت1: البلاط والتطعيم والفاصل — 1:5

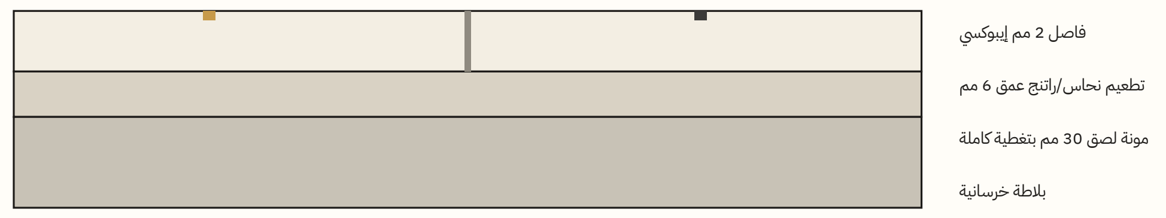

ت2: مرور النصل في الوجه — 1:5

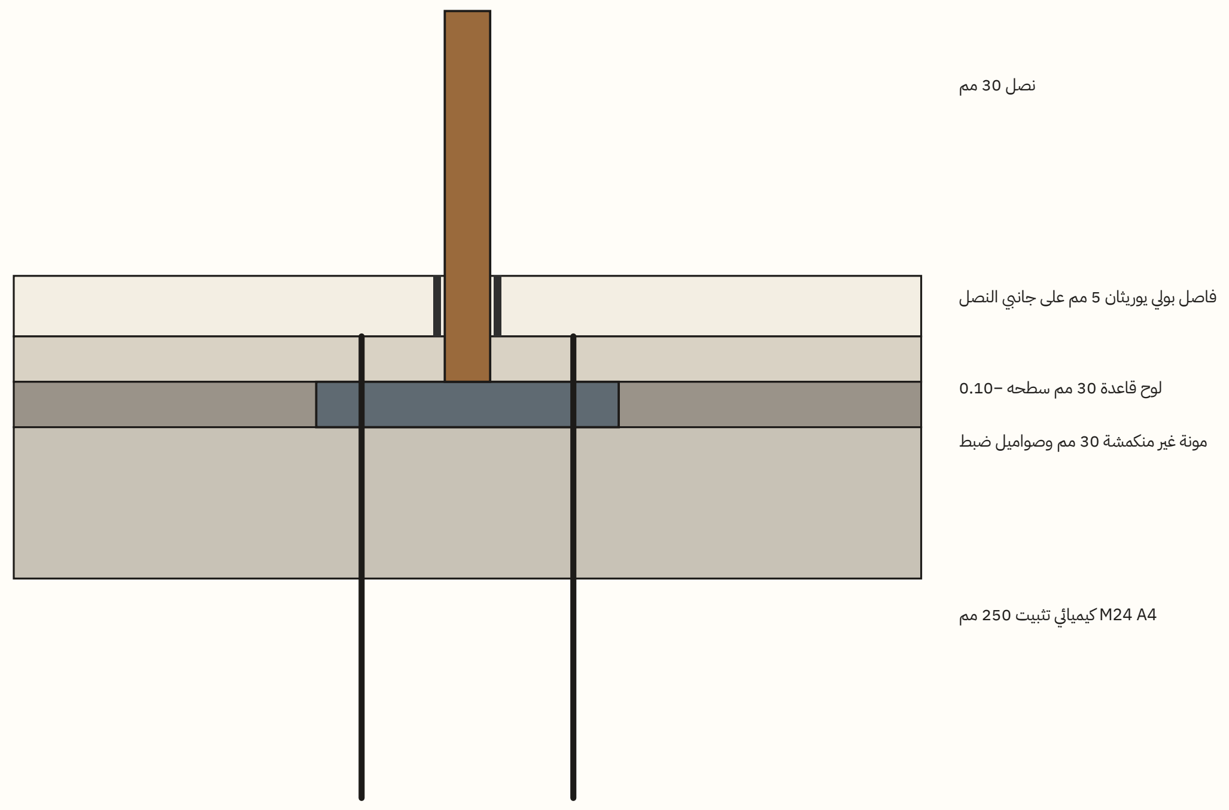
نصل 30 مم
فاصل بولي يوريثان 5 مم على جانبي النصل
لوح قاعدة 30 مم سطحه −0.10
مونة غير منكمشة 30 مم وصواميل ضبط
M24 A4 كيميائي تثبيت 250 مم

ت3: الحلقة والحافة والصرف — 1:5

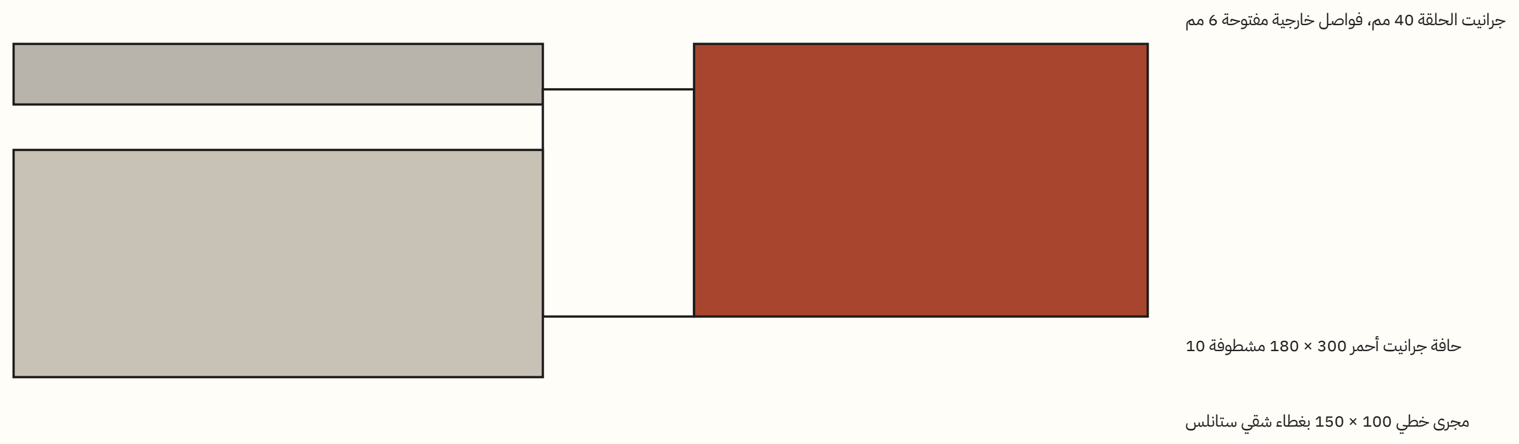
جرانيت الحلقة 40 مم، فواصل خارجية مفتوحة 6 مم
حافة جرانيت أحمر 300 × 180 مشطوفة 10
مجرى خطي 100 × 150 بغطاء شقي ستانلس