مشروع حدائق الفسطاط — المرحلة الثانية

منطقة الحدائق الترابية • البند SF-12: المزولة الشمسية

التصميم (أ): مزولة الشاخص القطبي

تقسيم بلاط الوجه وحلقة التقويم


180 بلاطة رخام و36 قطاع جرانيت
لكل قطعة رقم وملف قص

ملاحظات

- البلاط 900 × 900 × 40 ممر الأعمدة A… من القرب، والصفوف من الشمال.
- 108 بلاطة كاملة و72 بلاطة مفصوصة بالدائرة أو بشق النصل.
- كل بلاطة تُقص وتُحفر في المصنع من ملف: dxf/tiles/<الرقم>.dxf.
(الأصل ركبا الجنوبي الغربي، الوحدة mm، وتُكتب رقمها على ظهرها.
- شق النصل: 40 مم على خط الزوال من P5–20 إلى P6+20 مم.
- قطاعات الحلقة 36 × 10° من الشمال باتجاه عقارب الساعة (R36…R01).
- الفواصل 2 مم إيبوكسي بلون الحجر؛ لا فواصل تمدد داخل الوجه.

الموقع	ق = 31.2443° ش • λ = 30.0054° φ
مركز المزولة (الحزام الأحمر)	E 638413.3 • N 810602.7
القطر	14.50 م
مقياس الرسم	1:30
التاريخ	أكتوبر 2026
الحالة	مقترح تصميمي للمفاضلة

X-02

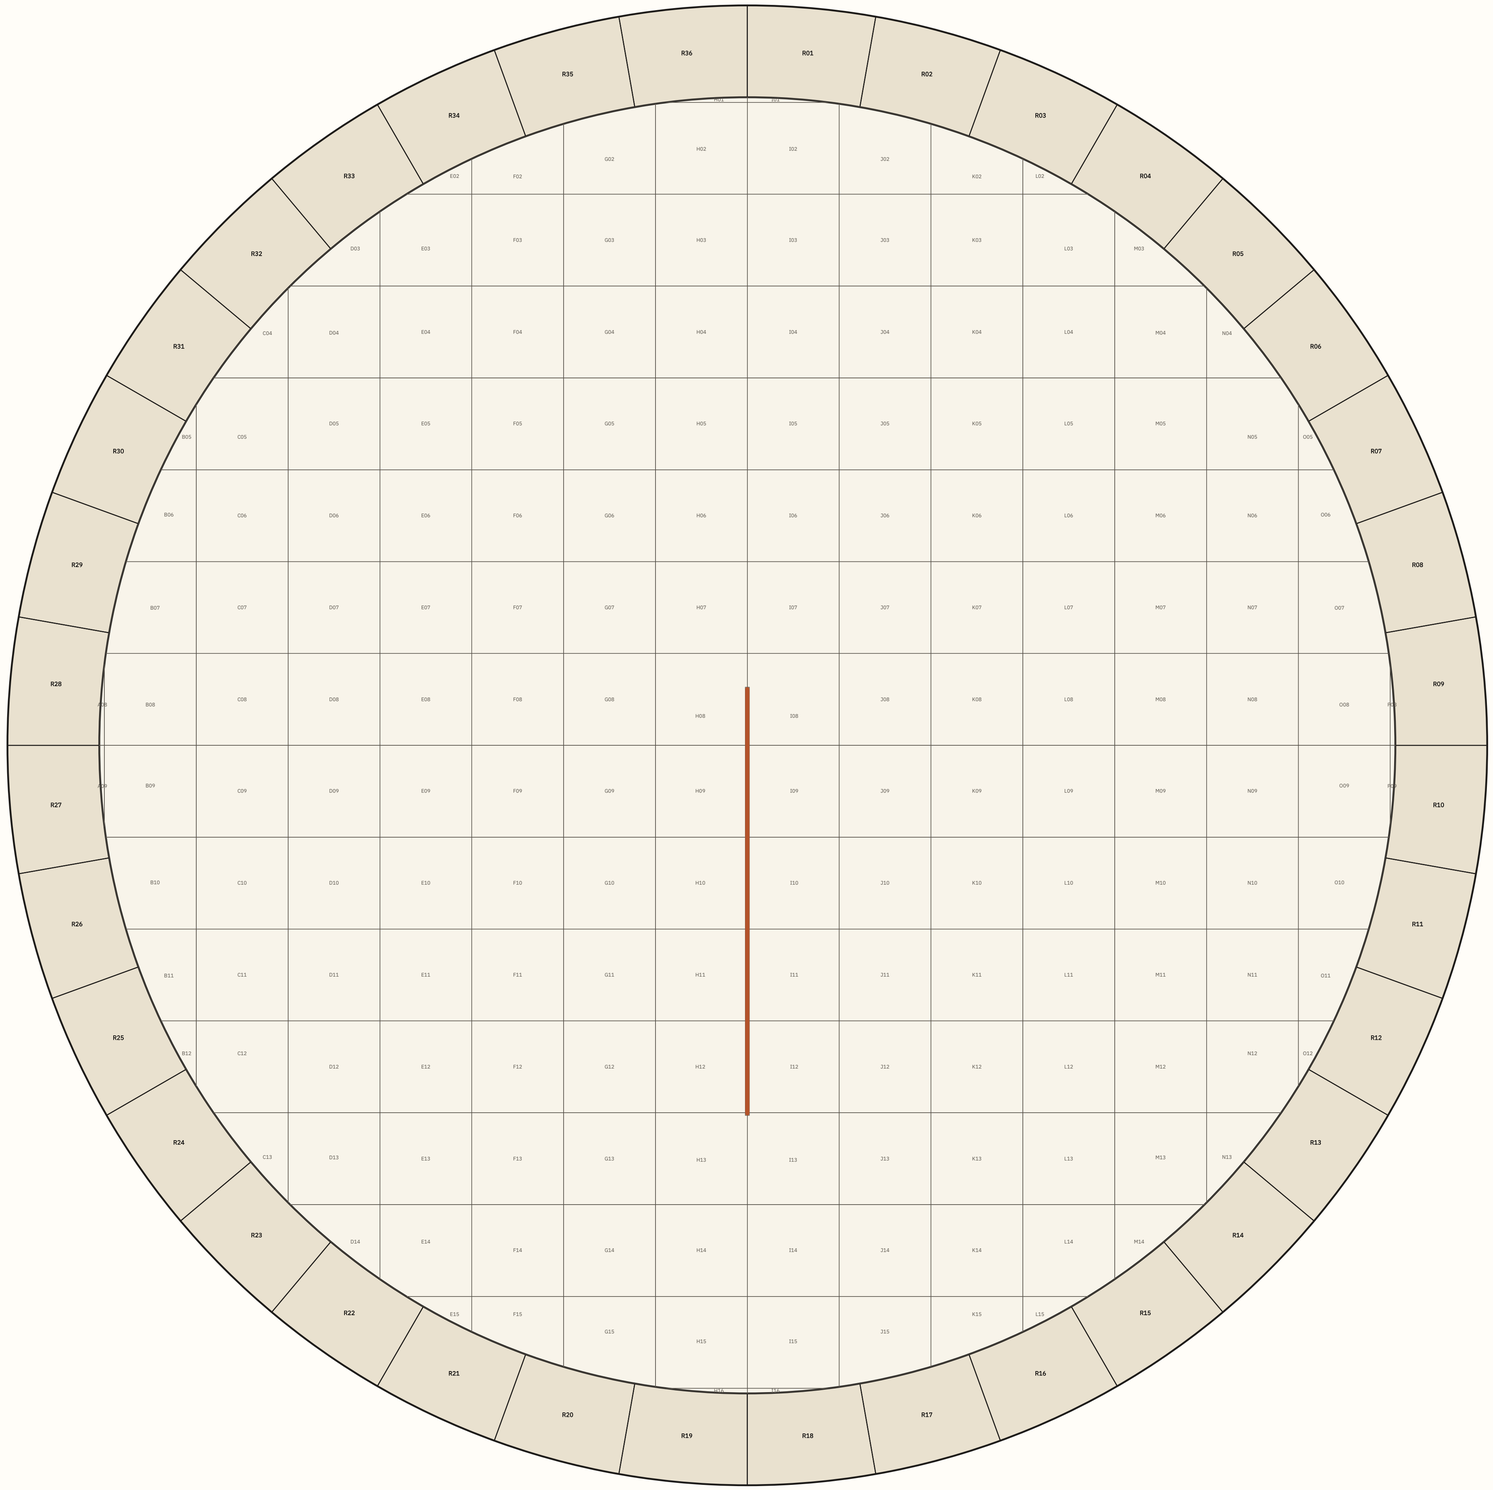

ملخص الكميات

البند	الكمية
بلاط الوجه (صافٍ)	126.5 م²
عدد البلاطات	180
قطاعات الحلقة	36 (38.5 م²)
طول الحافة	45.6 م
هالك مقترح للرخام	12%

الشمال الحقيقي

الشمال الشبكي منحرف 0.12° شرقًا

0 1 2 3 م