

مشروع حدائق الفسطاط – المرحلة الثانية

منطقة الحدائق الترابية • البند SF-12: المزولة الشمسية


التصميم (ج): بوابة عين الشمس

أرضية الضوء: المسقط الحسابي

بقعة الشمس من ثقب على ارتفاع 4.00 م
تقرأ توقيت مصر مباشرة بلا جداول

ملاحظات

• **التقرب:** قطر 50 سم في قرص برونزي مثالي، مركزه على ارتفاع 4.00 م فوق النقطة (0,00 - 3,00).
 • **بقعة المنحني:** صورة لقرص الشمس فطرها 9-5 سم.
 • **كل كائن (مناوية)** هو موضع البقعة عند ساعة رسمية (توقيت مصر) على مدار العام؛ الفرق التفاضلي نصف السنة الأول (يناير-يونيو) والمطلق الثاني (يوليو-ديسمبر).
 • **الخط الكبريتي:** شتوي، والصيفي شتوي في قوسين شمسيين.
 • **فارق الطول ومعادلة الزمن** داخلين في الرسم؛ لا تصحيح.
 • **خط الزوال (الدهلي):** أول الظل؛ والمقروء في أول العصر.
 • **الأرضية:** بإرث أو جرابيت أسود مطابق لخط الظل الضوء.
 • **المختلط وحساب** 6 م تحتها نصفاً مغطى بمسحوق

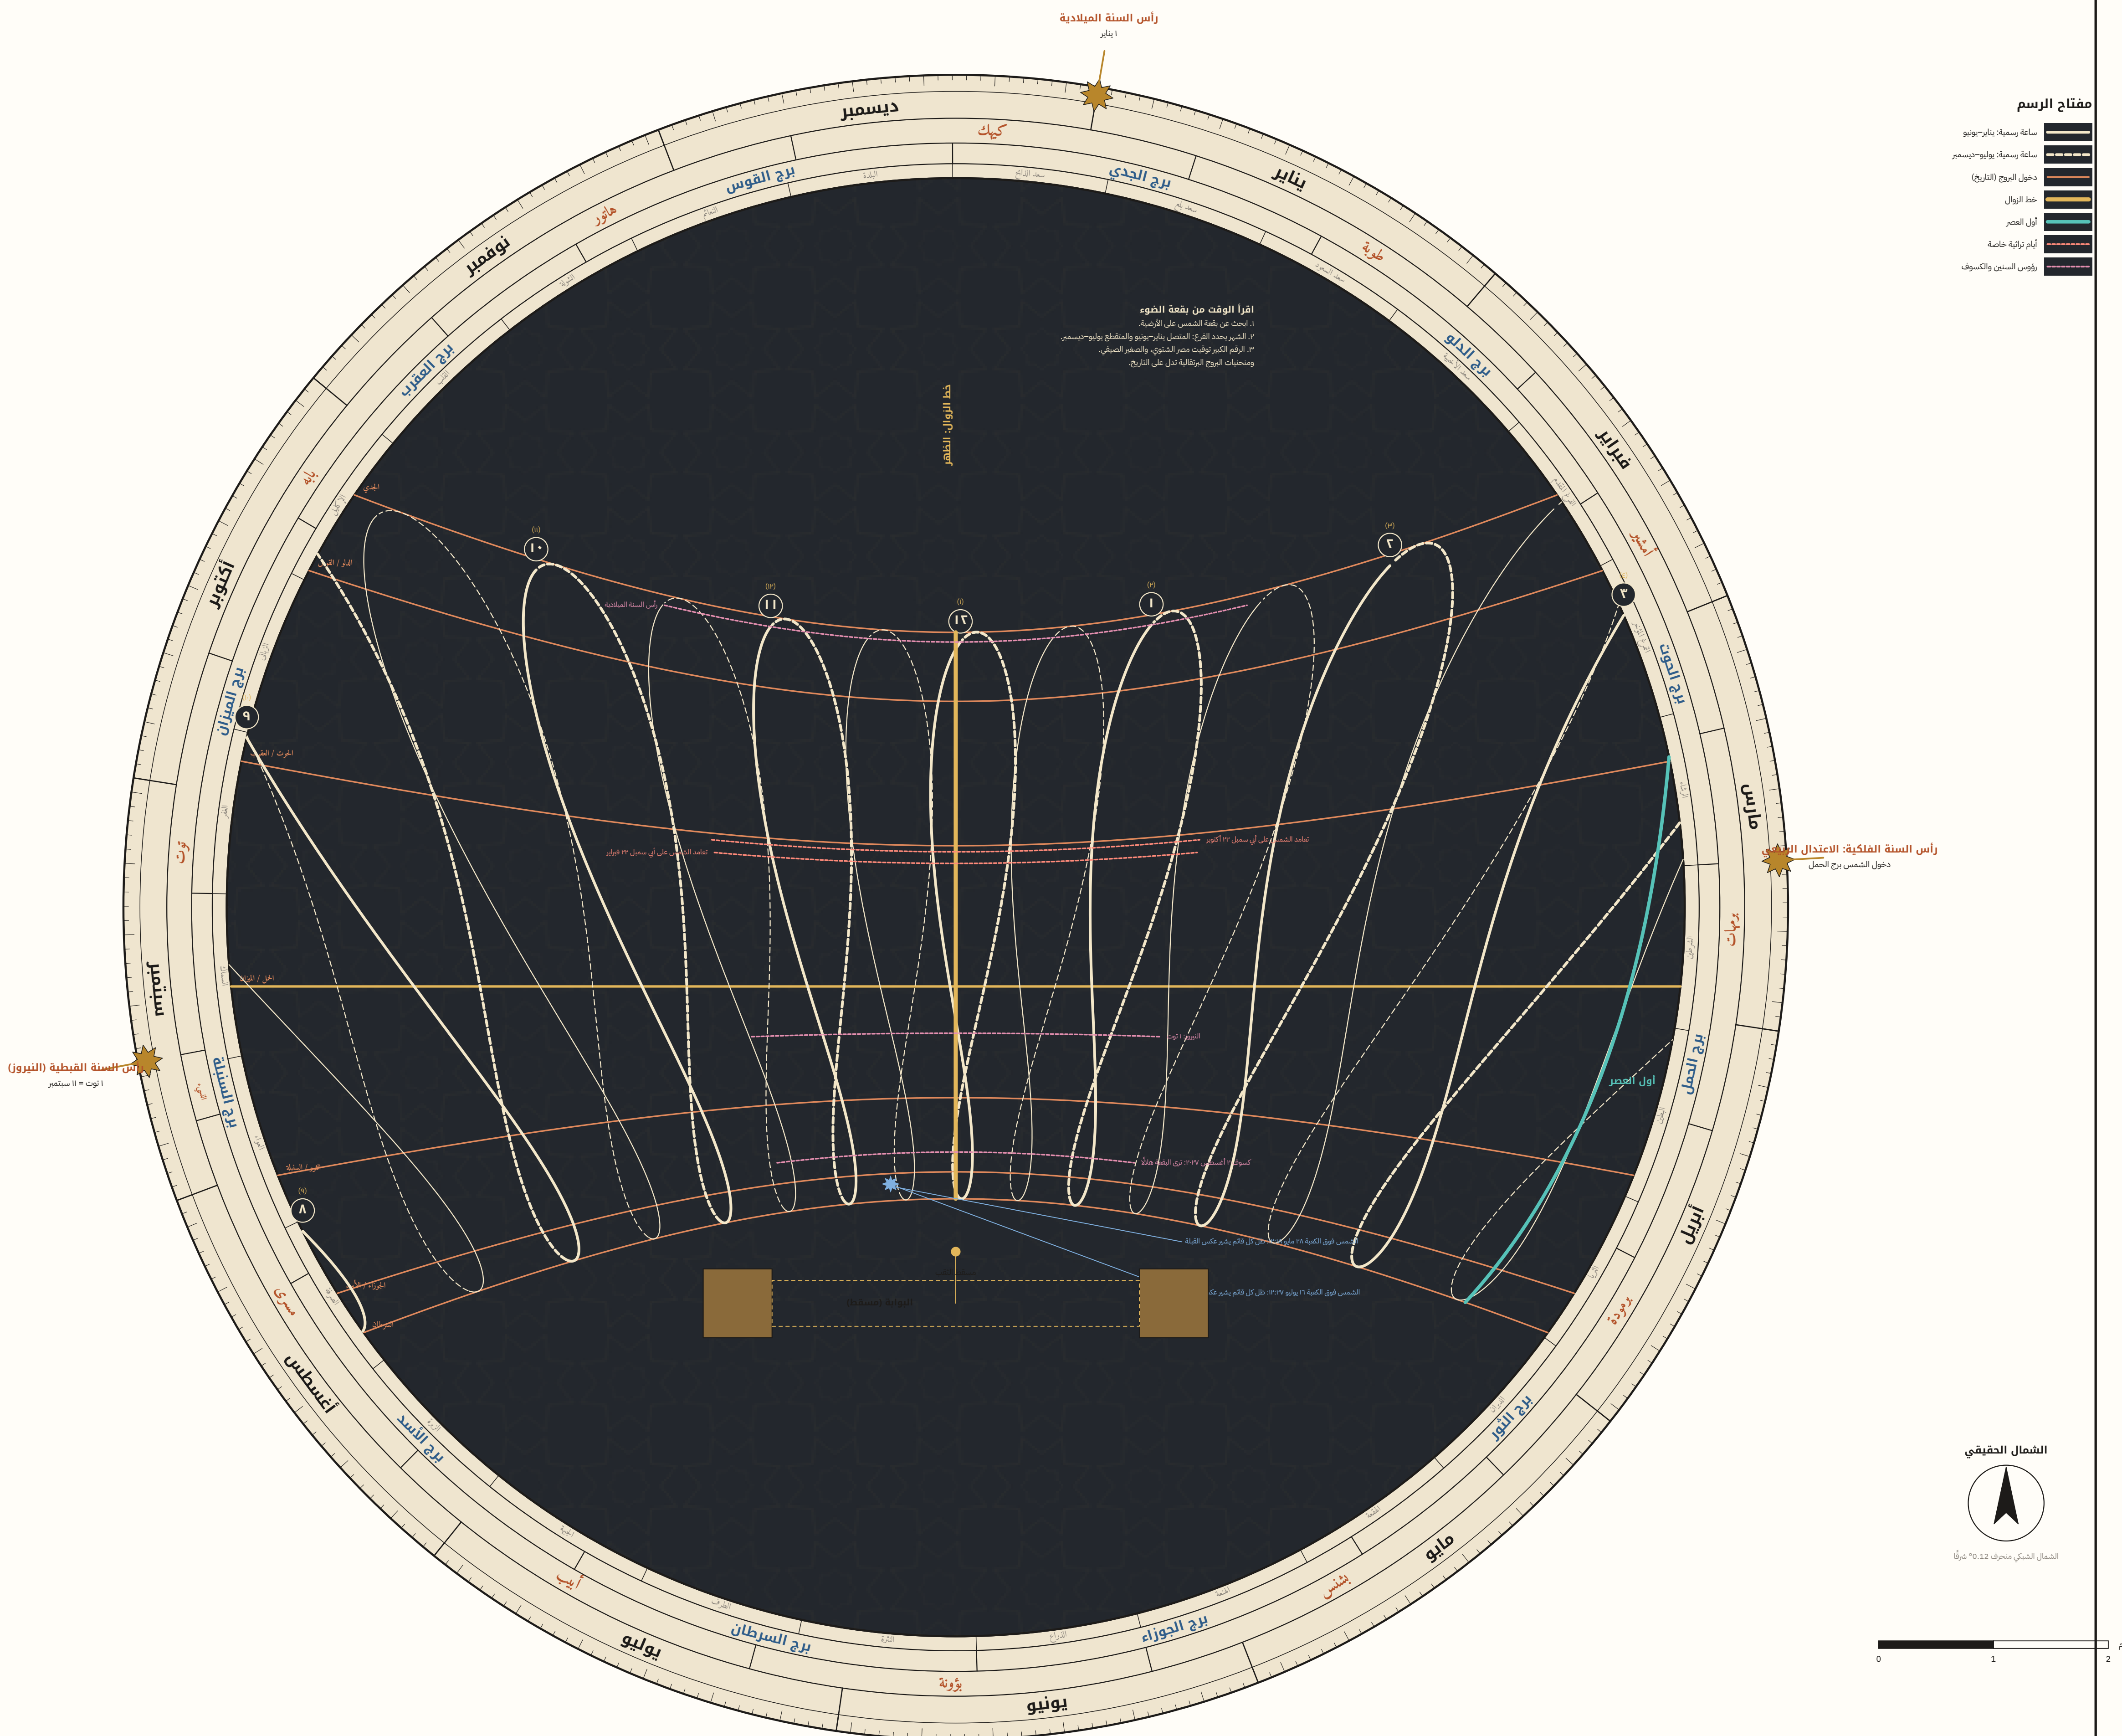

مفتاح الرسم

ساعة رسمية: يناير-يونيو

ساعة رسمية: بولو-ديسمبر

دخول، الخروج (التاريخ)

خط الزوال

191

أيام تراثية خاصة

رؤوس السنن والكسوف

أس السنة الفلكية: الاعتدال الربيعي
دخول الشمس برج الحمل

لشمال الحقیقی



الضمان الشيك منصرف 0.12° شرقاً

A horizontal number line with tick marks at 0, 1, and 2. The segment between 0 and 1 is filled with black ink.

الموقع

مركز المزولة (الحزام الأحمر)

القطر

مقياس الرسم

التاريخ

الحالة

ق = 31.2443° • ش = 30.0054° ϕ

E 638413.3 • N 810602.7

14.50 $\frac{1}{2}$

A1 على لوح) 1:30

2026 ۱۴۰۶

موفقاً نصيباً للمفاضلة

C-01